

VIÑAS NORTE

Renivelación de Losas — Resumen General

Manzana 7 y Manzana 14 · con hojas digitalizadas

Levantamiento de niveles de losa (renivelación) previo a la colocación de piso.
Se miden cotas en una malla de puntos; el promedio de desnivel define el espesor
de mortero premezclado y su volumen (m^3) por planta.

Convención: cota negativa = falta nivel (RELLENO) · cota positiva = sobra (CORTE).
Cada planta incluye su HOJA DIGITALIZADA y la hoja de campo original.

Fecha: 01/07/2026

Levantó: Mauricio Gastelum Mora

Resumen de renivelación


Lote	Mza	Modelo	Planta	Área m²	Prom. cm	Mortero m³	Estado
L33	M14	Cabernet	P.B.	72.63	1.84	1.34	Renivelado
L33	M14	Cabernet	P.A.	65.21	2.94	1.88	Renivelado
L9	M7	Merlot	P.B.	74.86	3.10	2.56	Renivelado (completo)
L9	M7	Merlot	P.A.	58.25	3.40	1.93	
L10	M7	Merlot	P.B.	74.86	1.20	—	No renivelado
L10	M7	Merlot	P.A.	58.25	2.50	1.50	Renivelado
L19	M7	Chardonnay	P.A.	59.86	3.40	1.50	Renivelado
L19	M7	Chardonnay	P.B.	85.79	1.71	1.46	Renivelado
L17	M7	Chardonnay	P.B.	85.79	1.45	1.28	Renivelado
L17	M7	Chardonnay	P.A.	59.86	2.24	2.59	Por confirmar
					TOTAL	13.45	

Notas y verificación de hojas de campo

- Verificación foto por foto (encabezado con zoom + aritmética + geometría del plano): f1=L33 P.A. · f2=L33 P.B. · f3=L9 P.B. (V=2.56) · f4=L9 P.A. (V=1.93; la hoja dice 'P.B.' por error) · f5=L10 P.B. (V=1.06) · f6 y f7=MISMA hoja, L10 P.A. (V=1.46).
- L10 M7: P.B. levantada (1.06 m³) pero NO se renivela (prom. 1.2 cm, mínimo). P.A. sí: V hoja 1.46 ≈ 1.5 m³.
- L19 y L17 (Chardonnay): datos dictados del levantamiento; hojas de campo NO incluidas en las fotos recibidas.
- Terrazas (L33/L34 Cabernet, L17 Chardonnay): sin colar; NO entran en la renivelación.
- ⚠ L17 M7 P.A.: 2.59 m³ no cuadra con 2.24 cm × 59.86 m² (≈1.34 m³). Por confirmar; fuera del total.
- L34 M14 (Cabernet): PENDIENTE — se agrega cuando llegue su levantamiento.


LOTE 33 · MZA 14 (CABERNET) — PLANTA BAJA

Hoja digitalizada · 72.63 m² · prom. 1.84 cm · mortero 1.34 m³

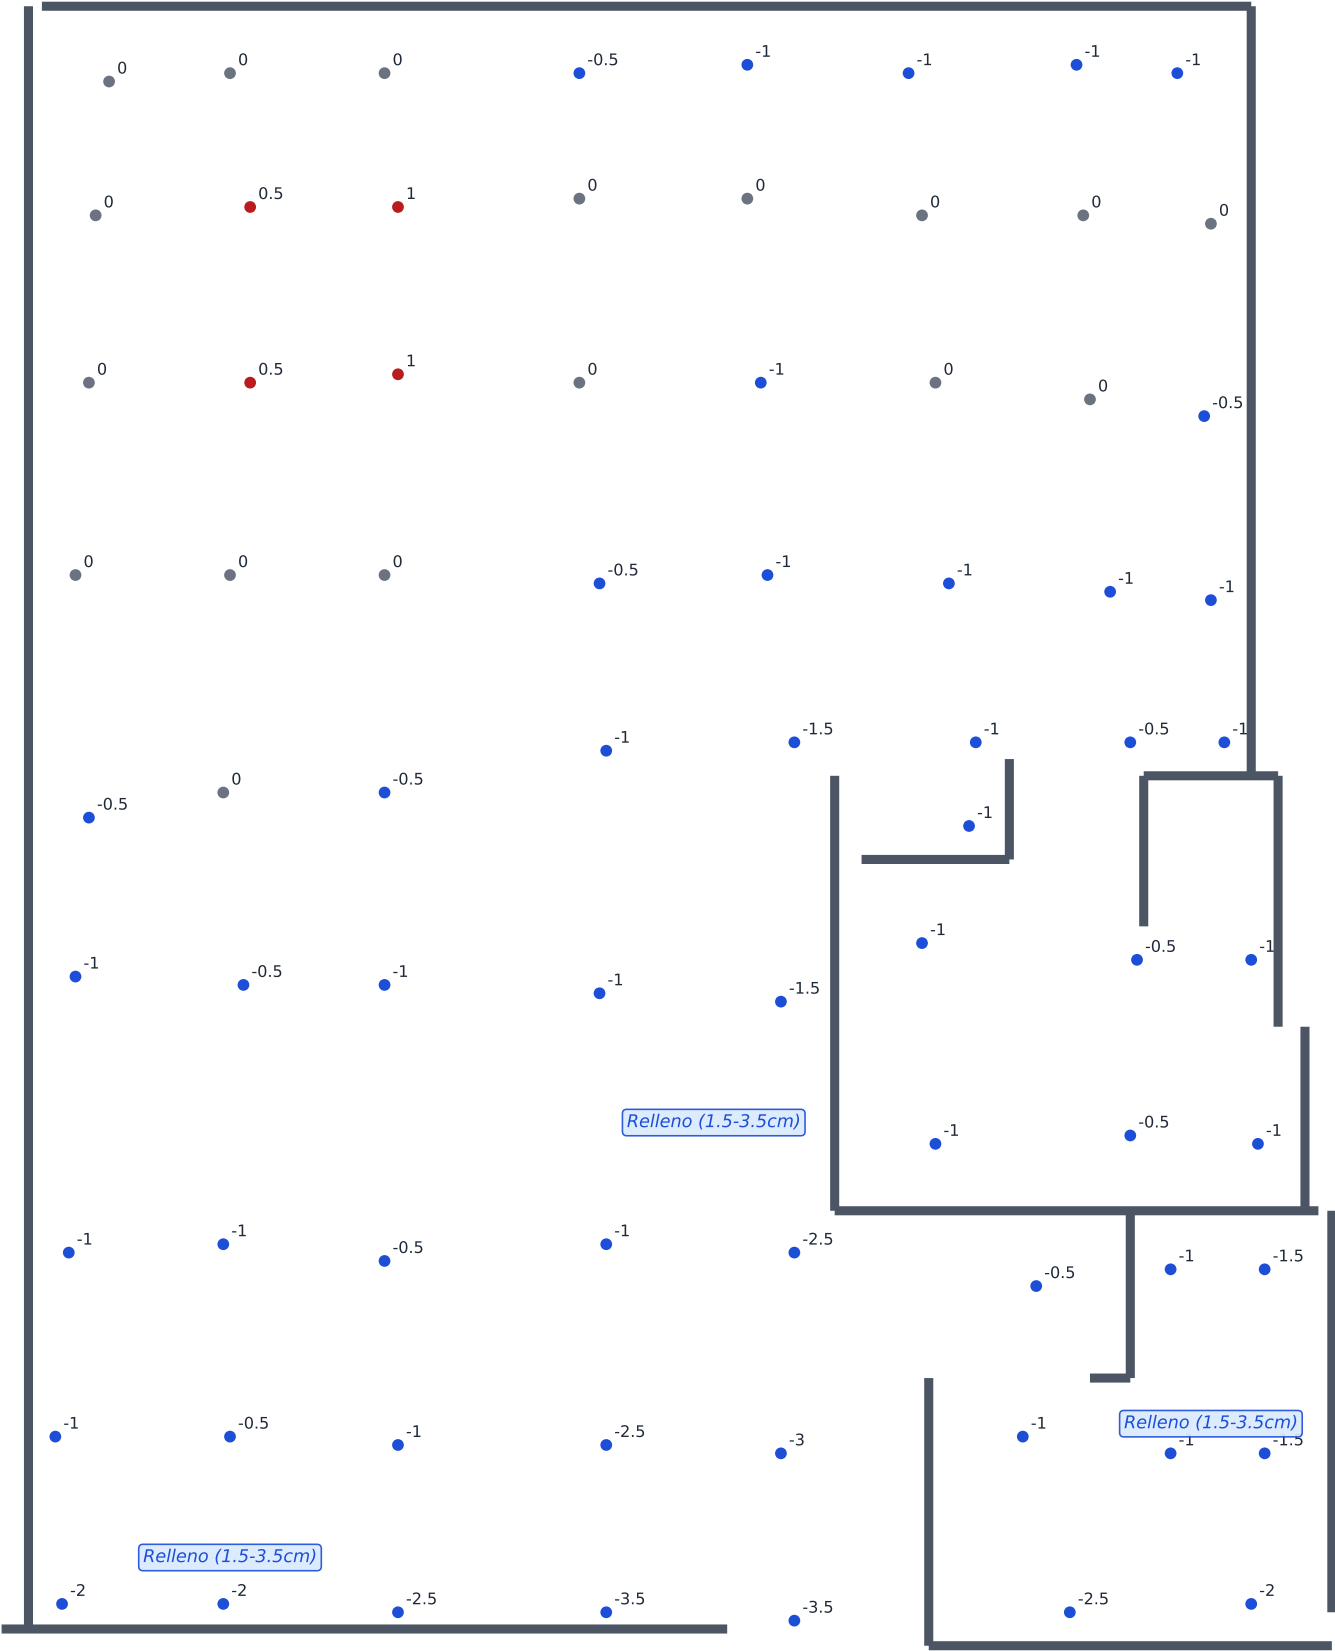


- Relleno (cota negativa: falta nivel)
- A nivel (0)
- ☐ Vacío / losa sin colar
- Corte (cota positiva: sobra)
- ☐ Escalera

Hoja de campo original

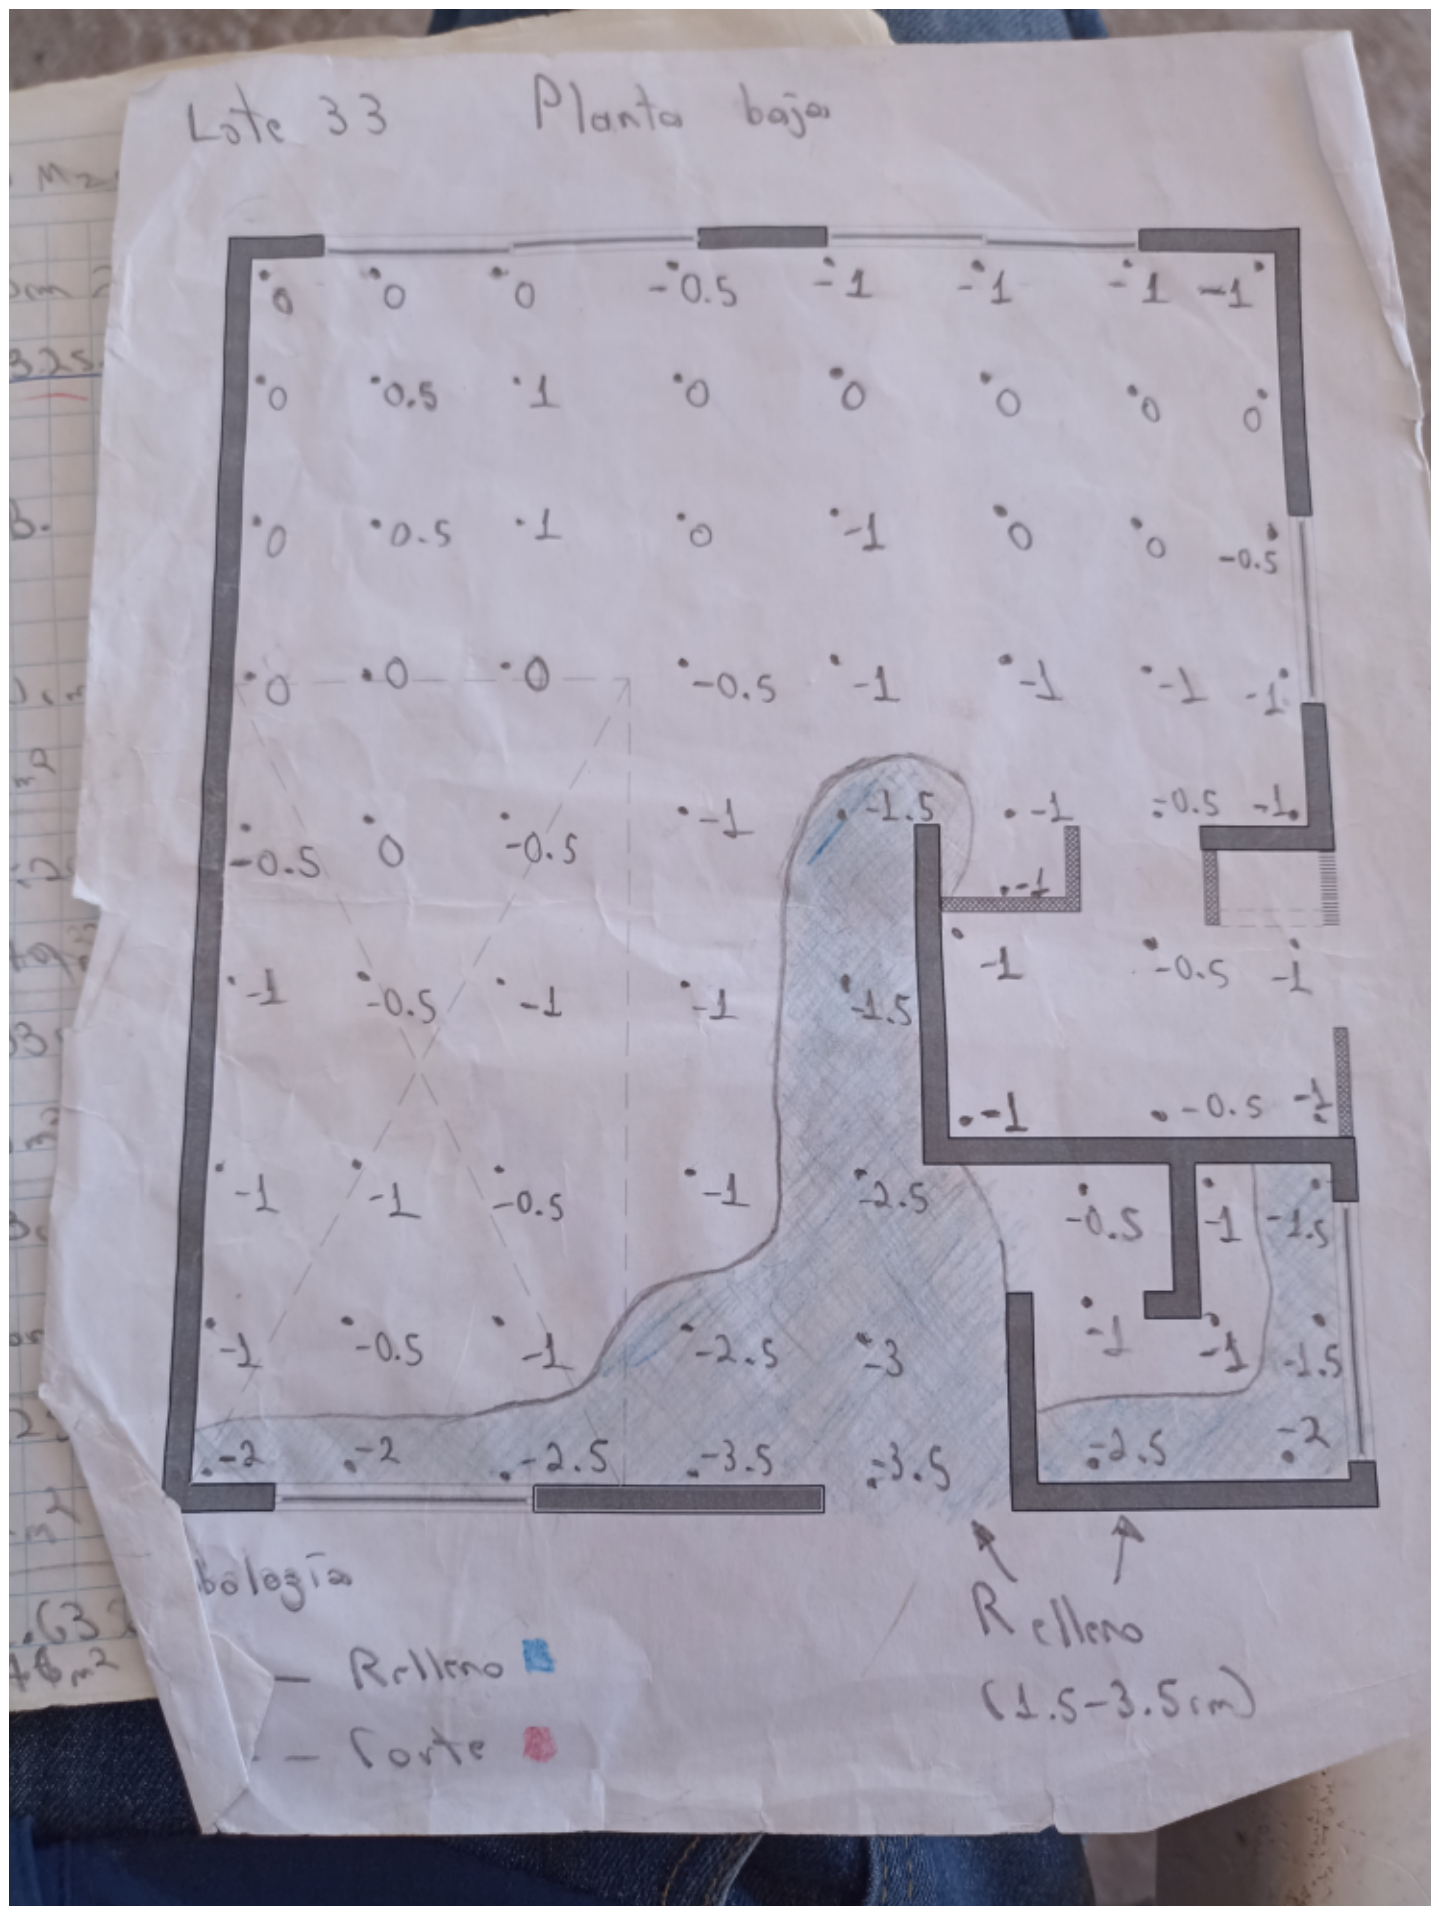


LOTE 33 · MZA 14 (CABERNET) — PLANTA ALTA

Hoja digitalizada · 65.21 m² · prom. 2.94 cm · mortero 1.88 m³

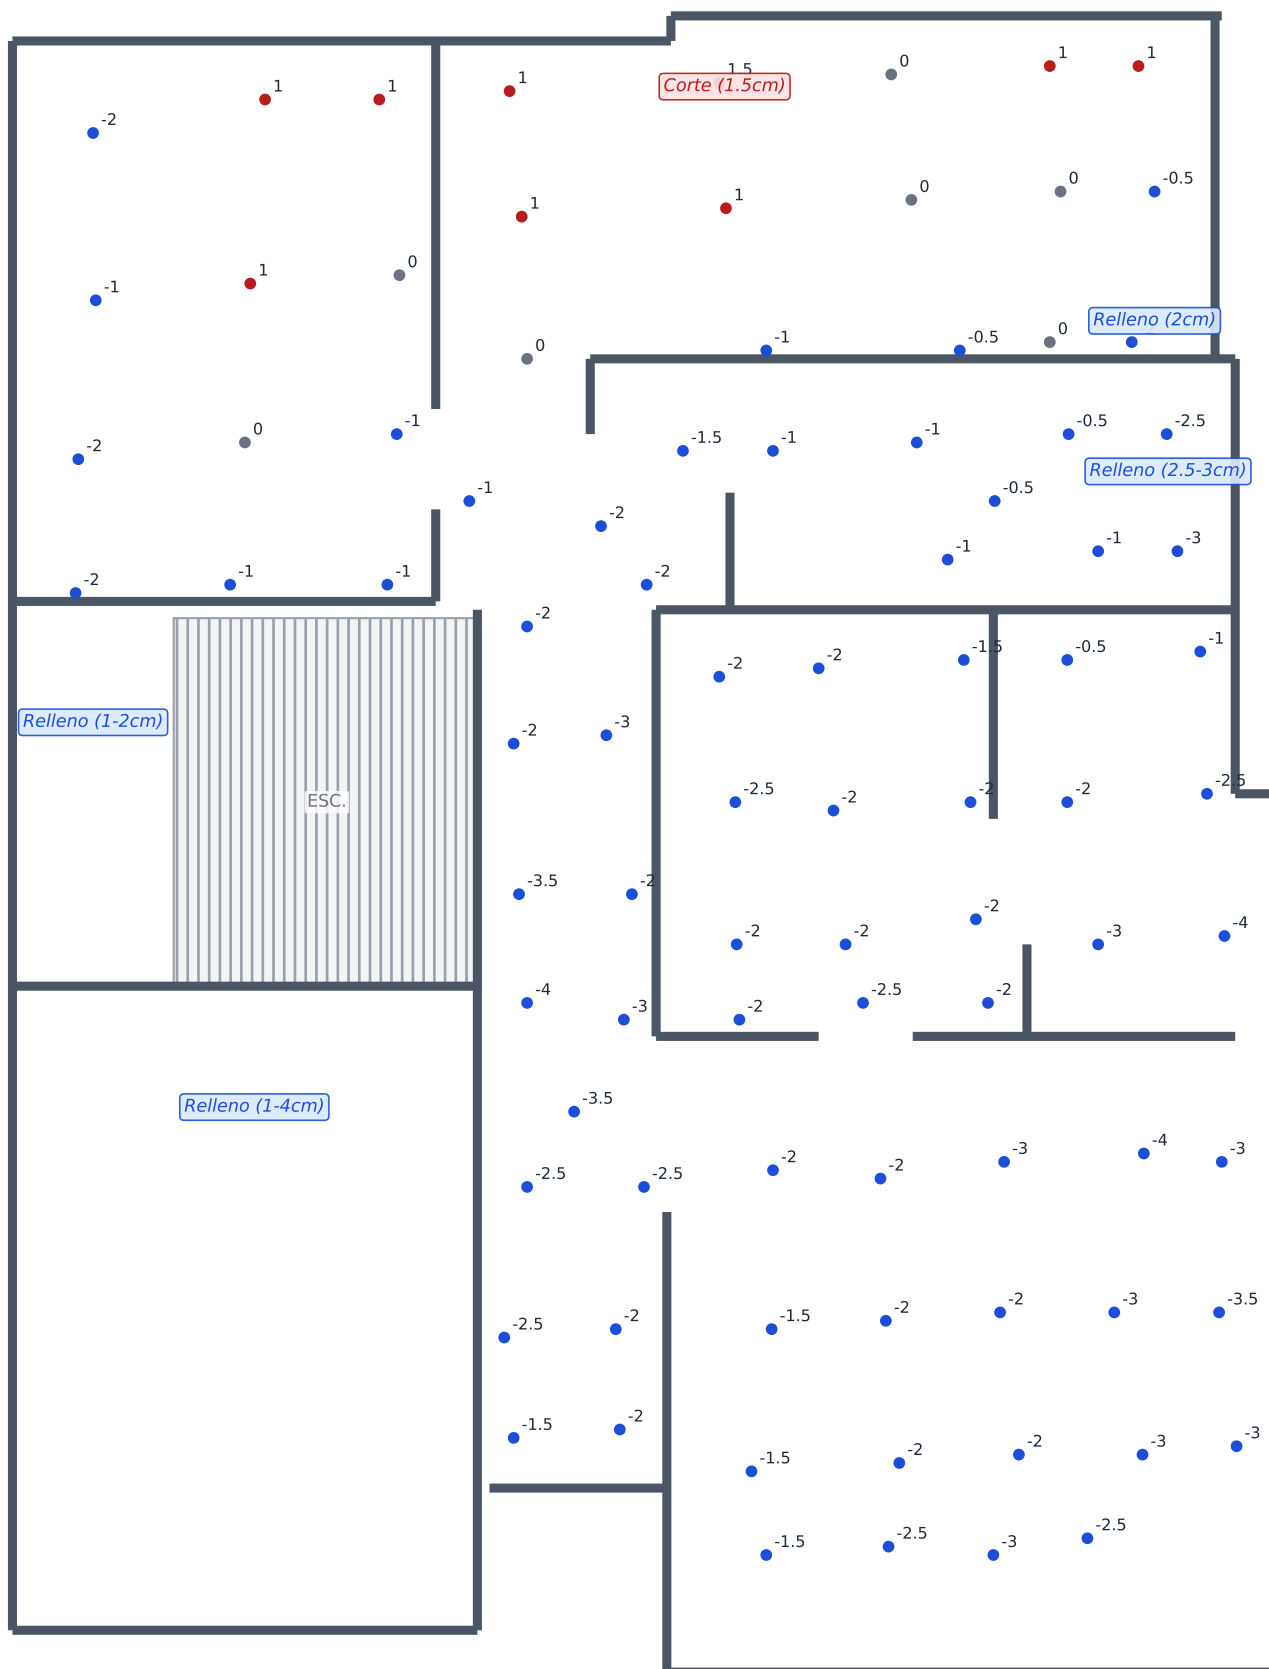


- Relleno (cota negativa: falta nivel)
- Corte (cota positiva: sobra)
- A nivel (0)
- ▨ Vacío / losa sin colar
- Escalera

Hoja de campo original

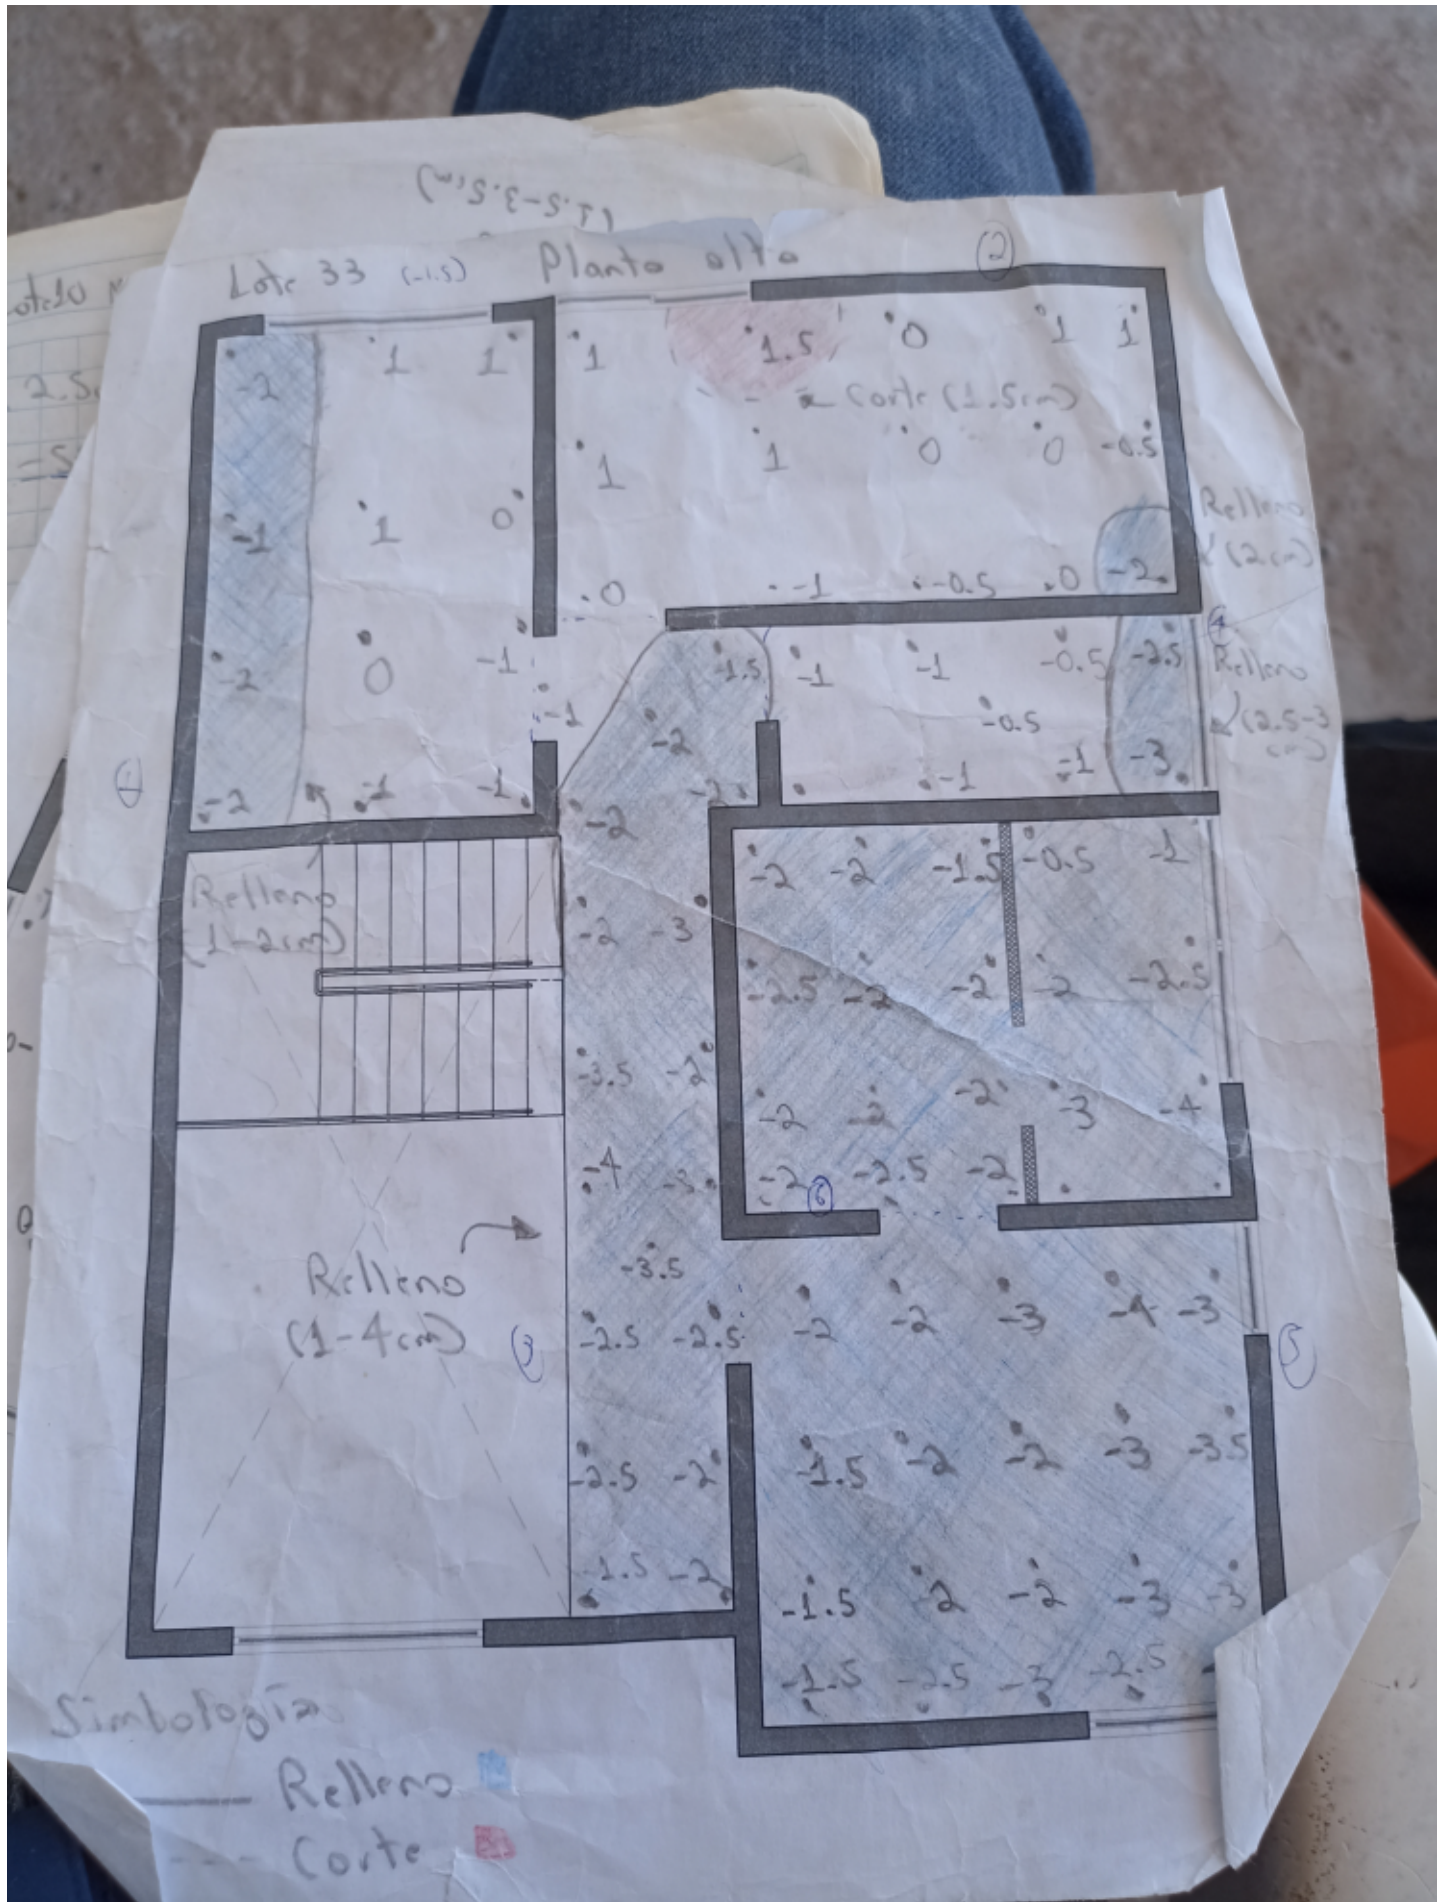


LOTE 9 · MZA 7 (MERLOT) — PLANTA BAJA

Hoja digitalizada · 74.86 m² · prom. 3.10 cm · mortero 2.56 m³ · hoja: V=2.56 m³

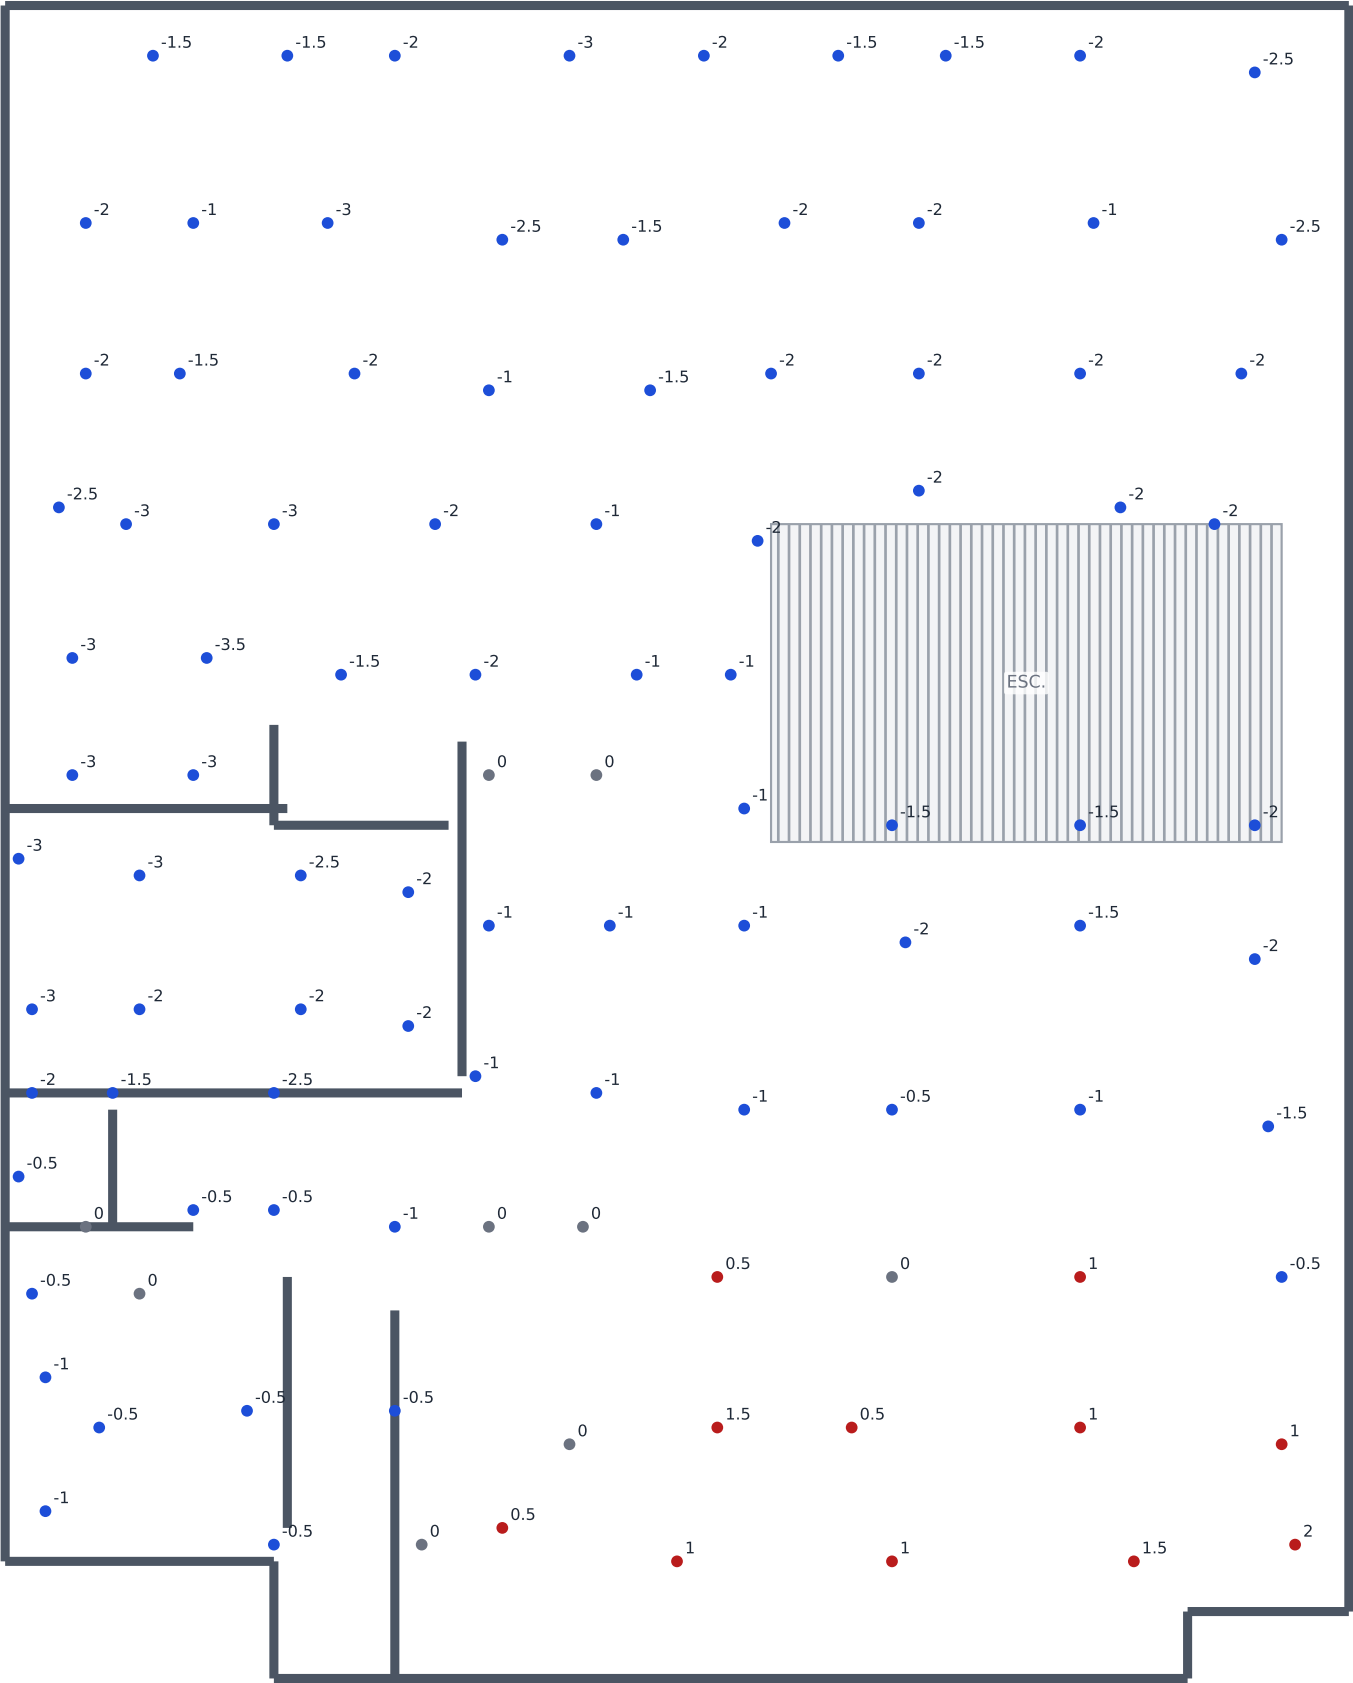


- Relleno (cota negativa: falta nivel)
- A nivel (0)
- ▨ Vacío / losa sin colar
- Corte (cota positiva: sobra)
- ▨ Escalera

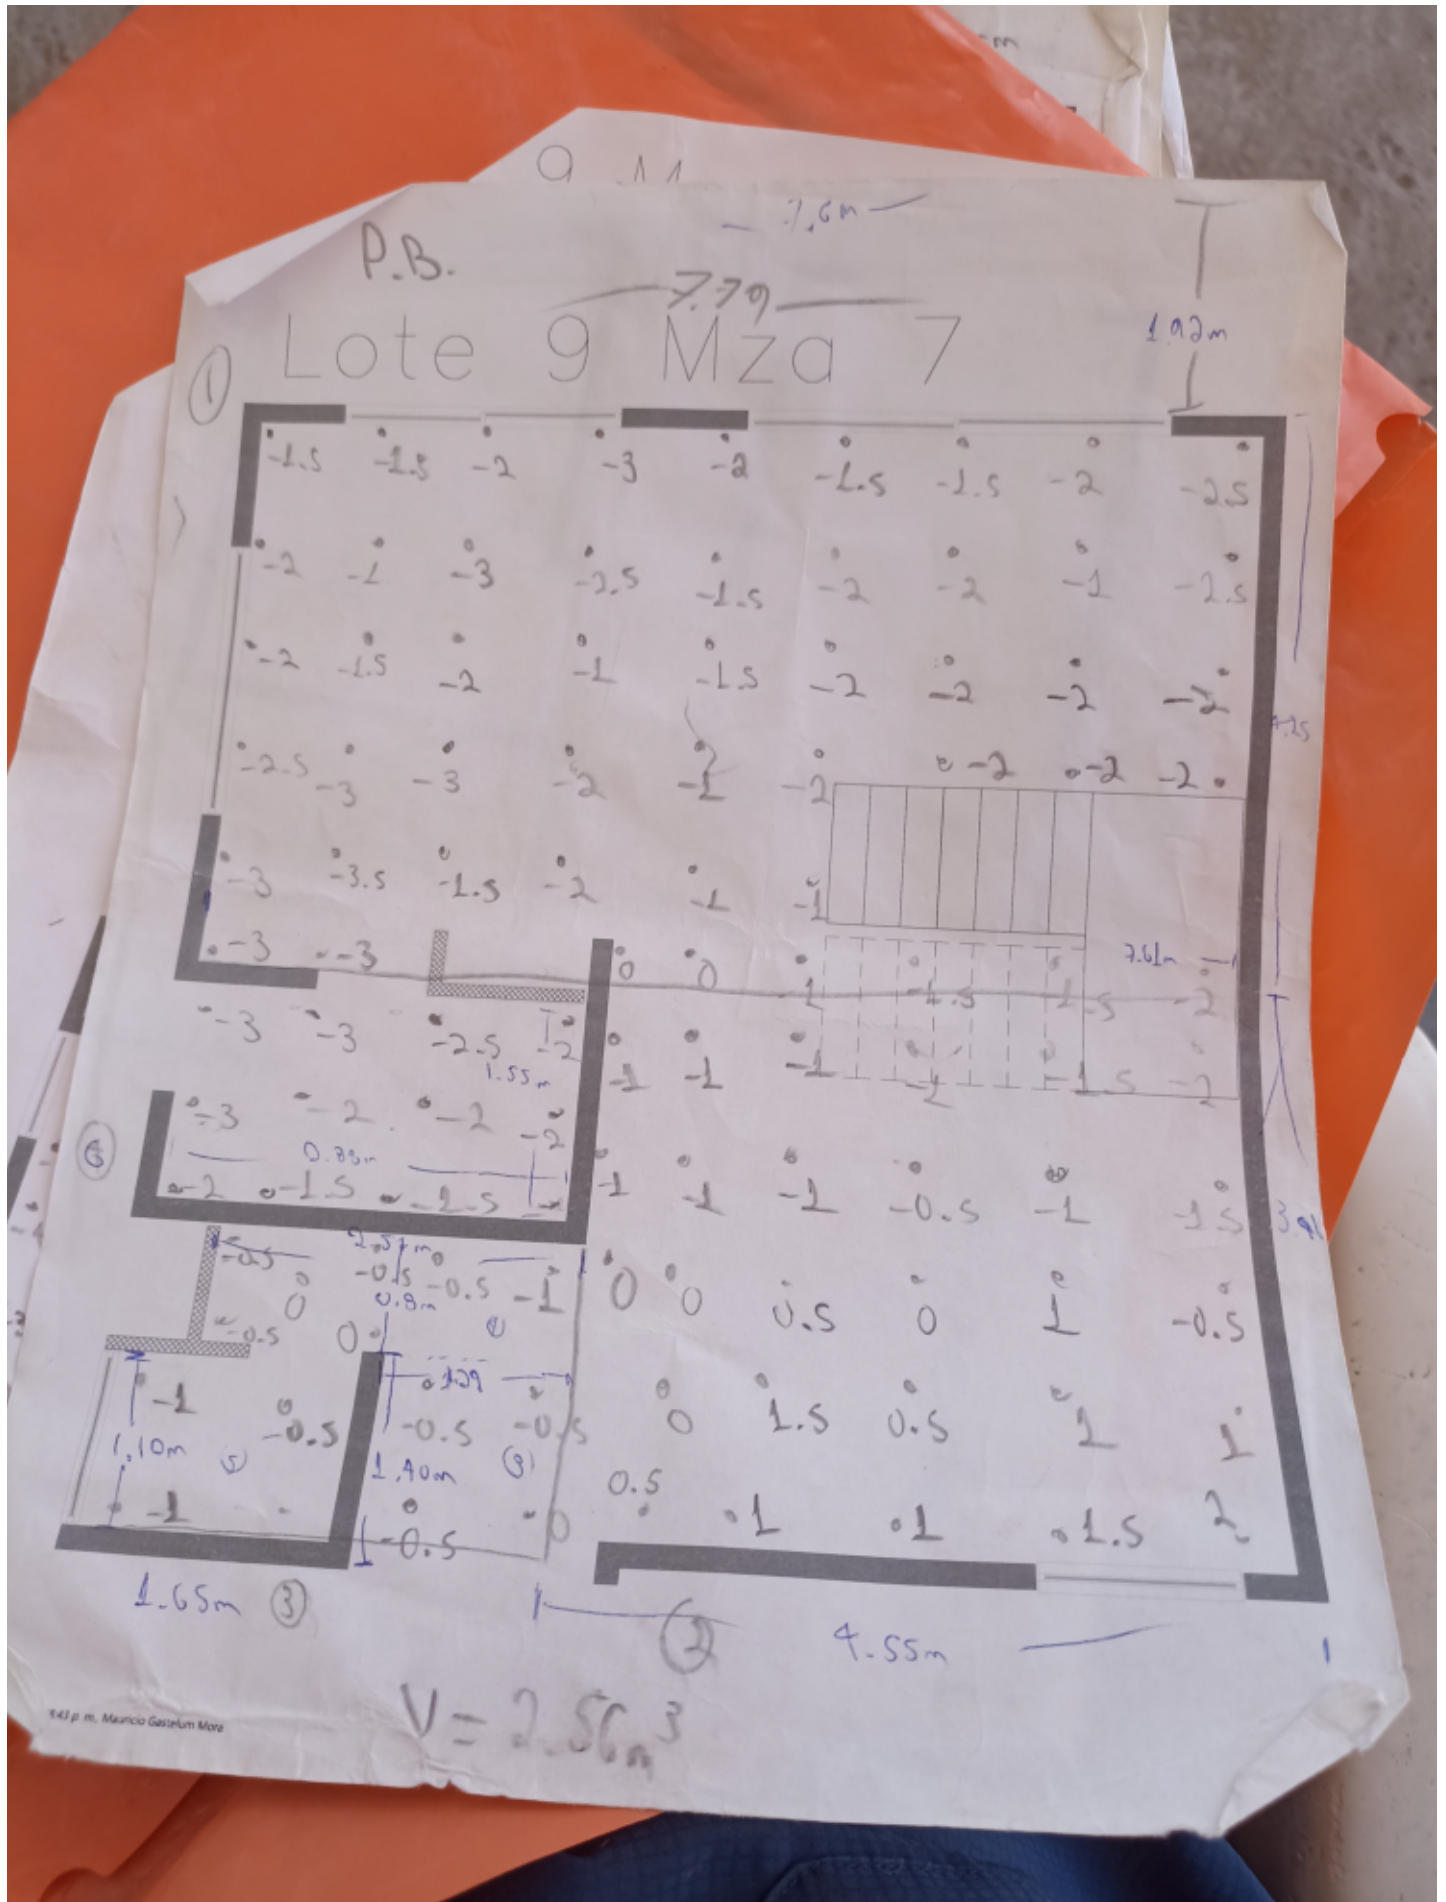

LOTE 9 · MZA 7 (MERLOT) — PLANTA ALTA

Hoja digitalizada · 58.25 m² · prom. 3.40 cm · mortero 1.93 m³ · hoja: V=1.93 m³

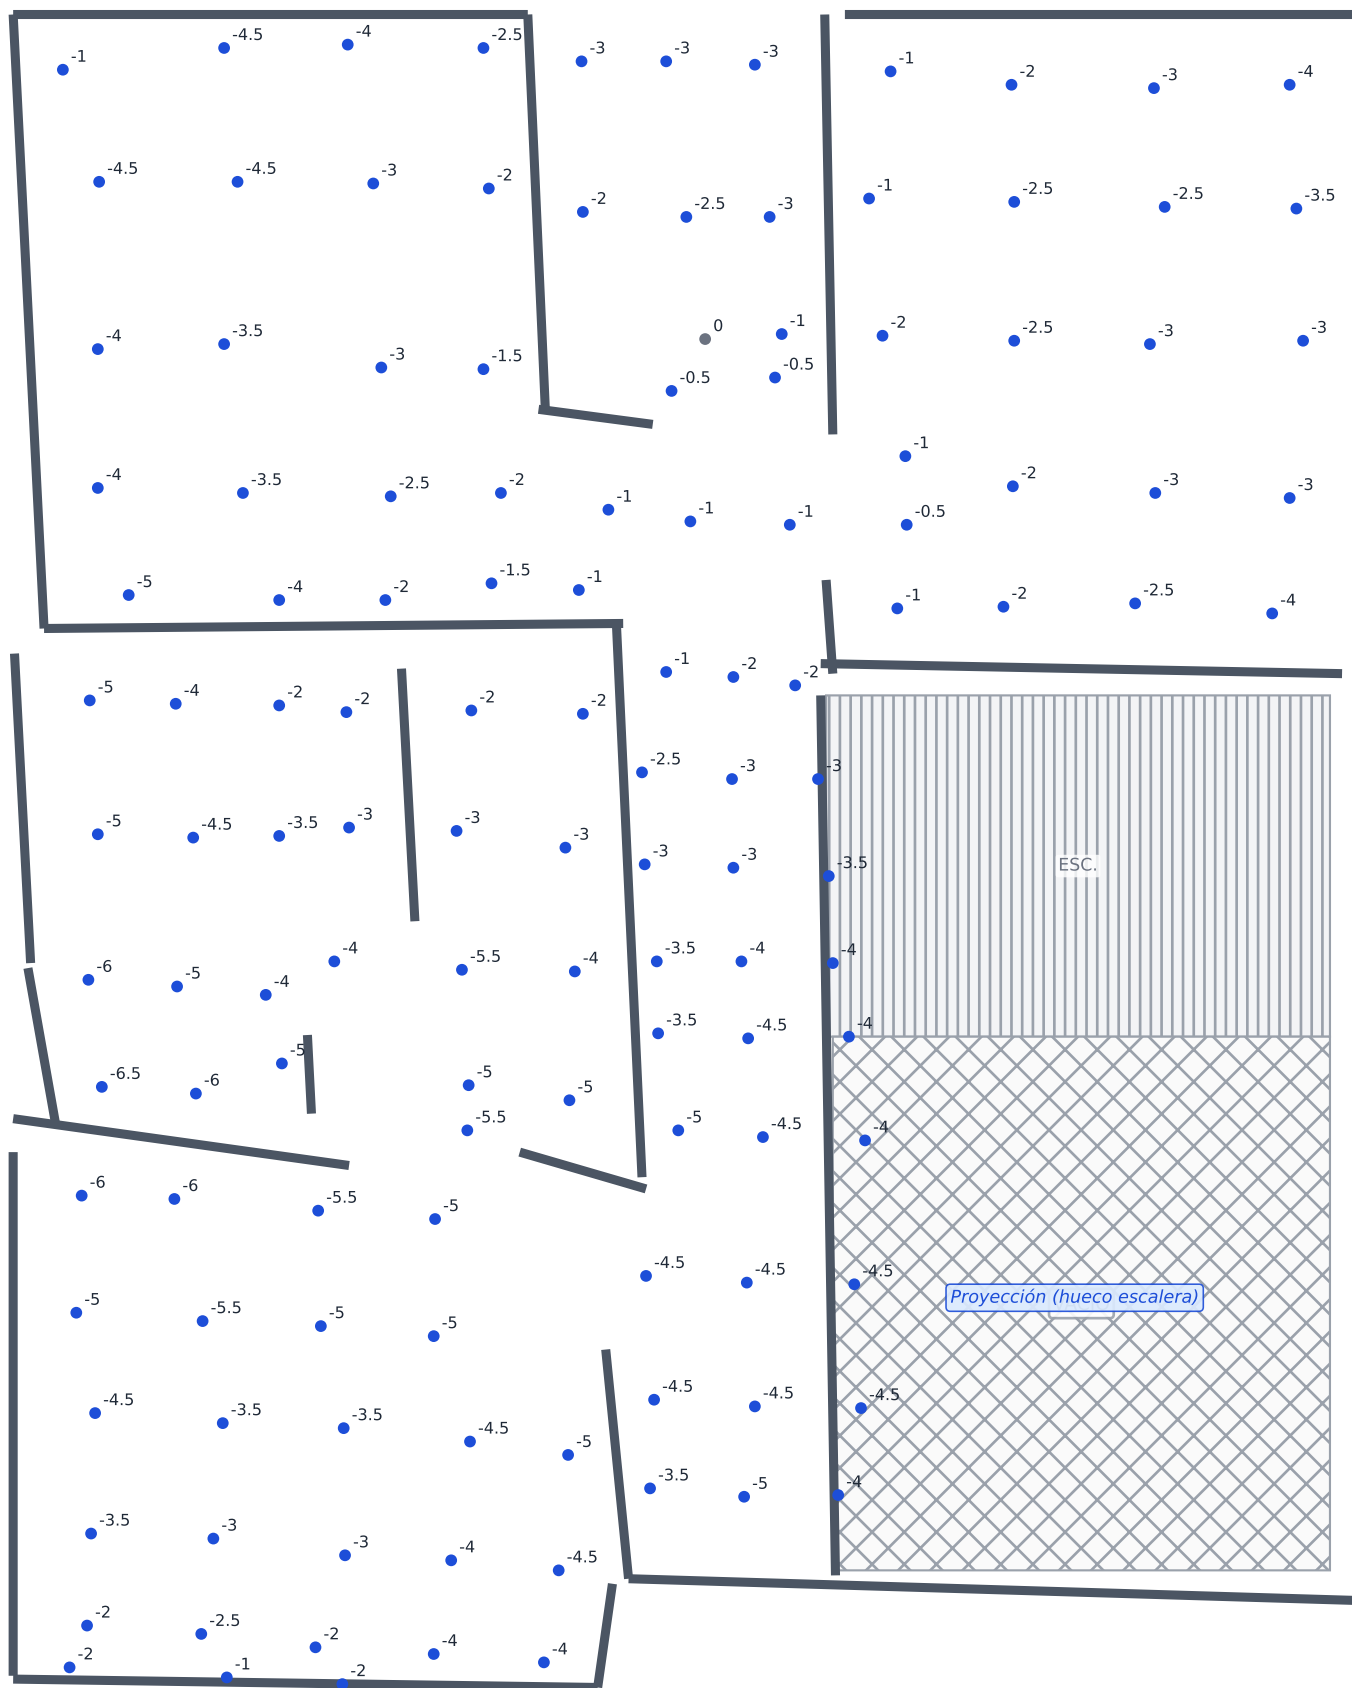


- Relleno (cota negativa: falta nivel) ● A nivel (0) ▨ Vacío / losa sin colar
- Corte (cota positiva: sobra) ▨ Escalera




Hoja digitalizada · 74.86 m² · prom. 1.20 cm · mortero levantada, sin ejecutar · hoja: V=1.06 m³

Hoja digitalizada · 74.86 m² · prom. 1.20 cm · mortero levantada, sin ejecutar · hoja: V=1.06 m³

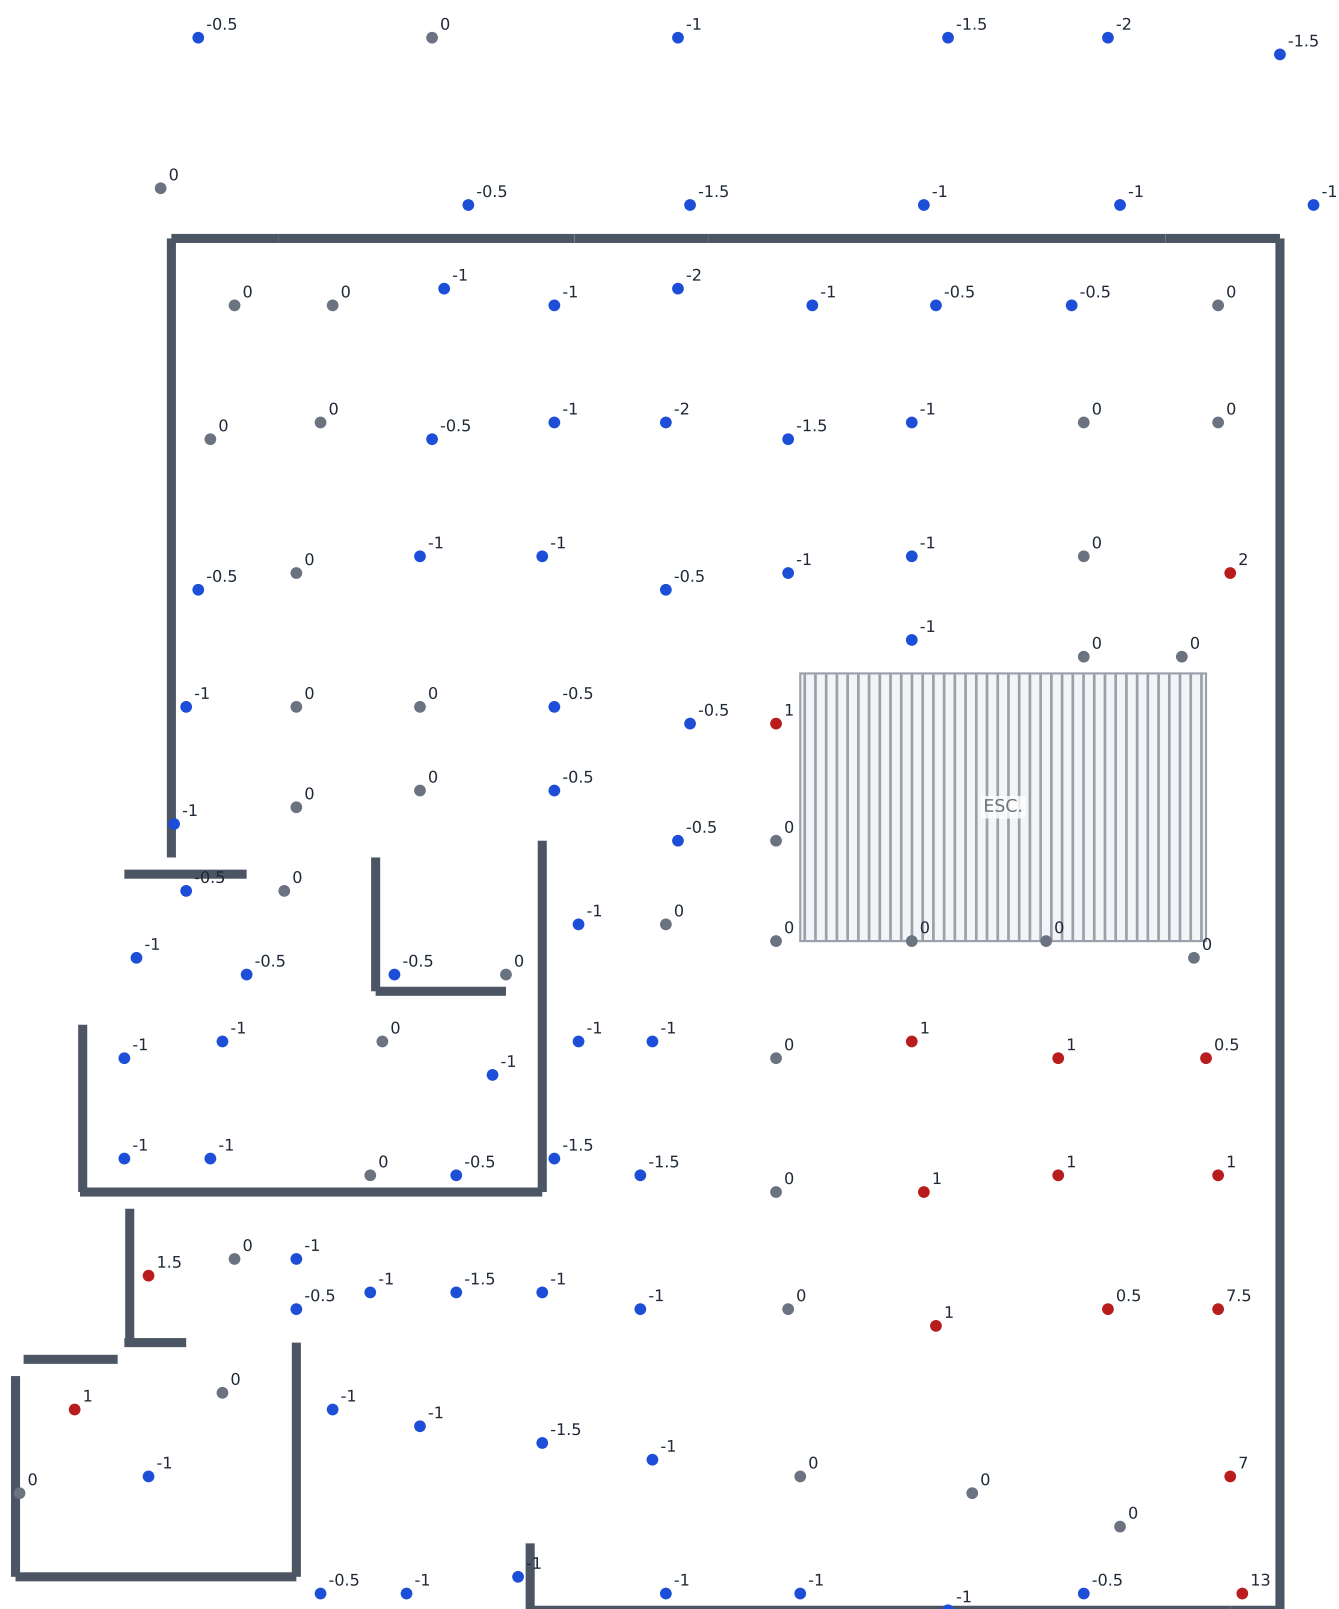


- Relleno (cota negativa: falta nivel)
 ● A nivel (0)
  Vacío / losa sin colar
● Corte (cota positiva: sobra)
 Escalera

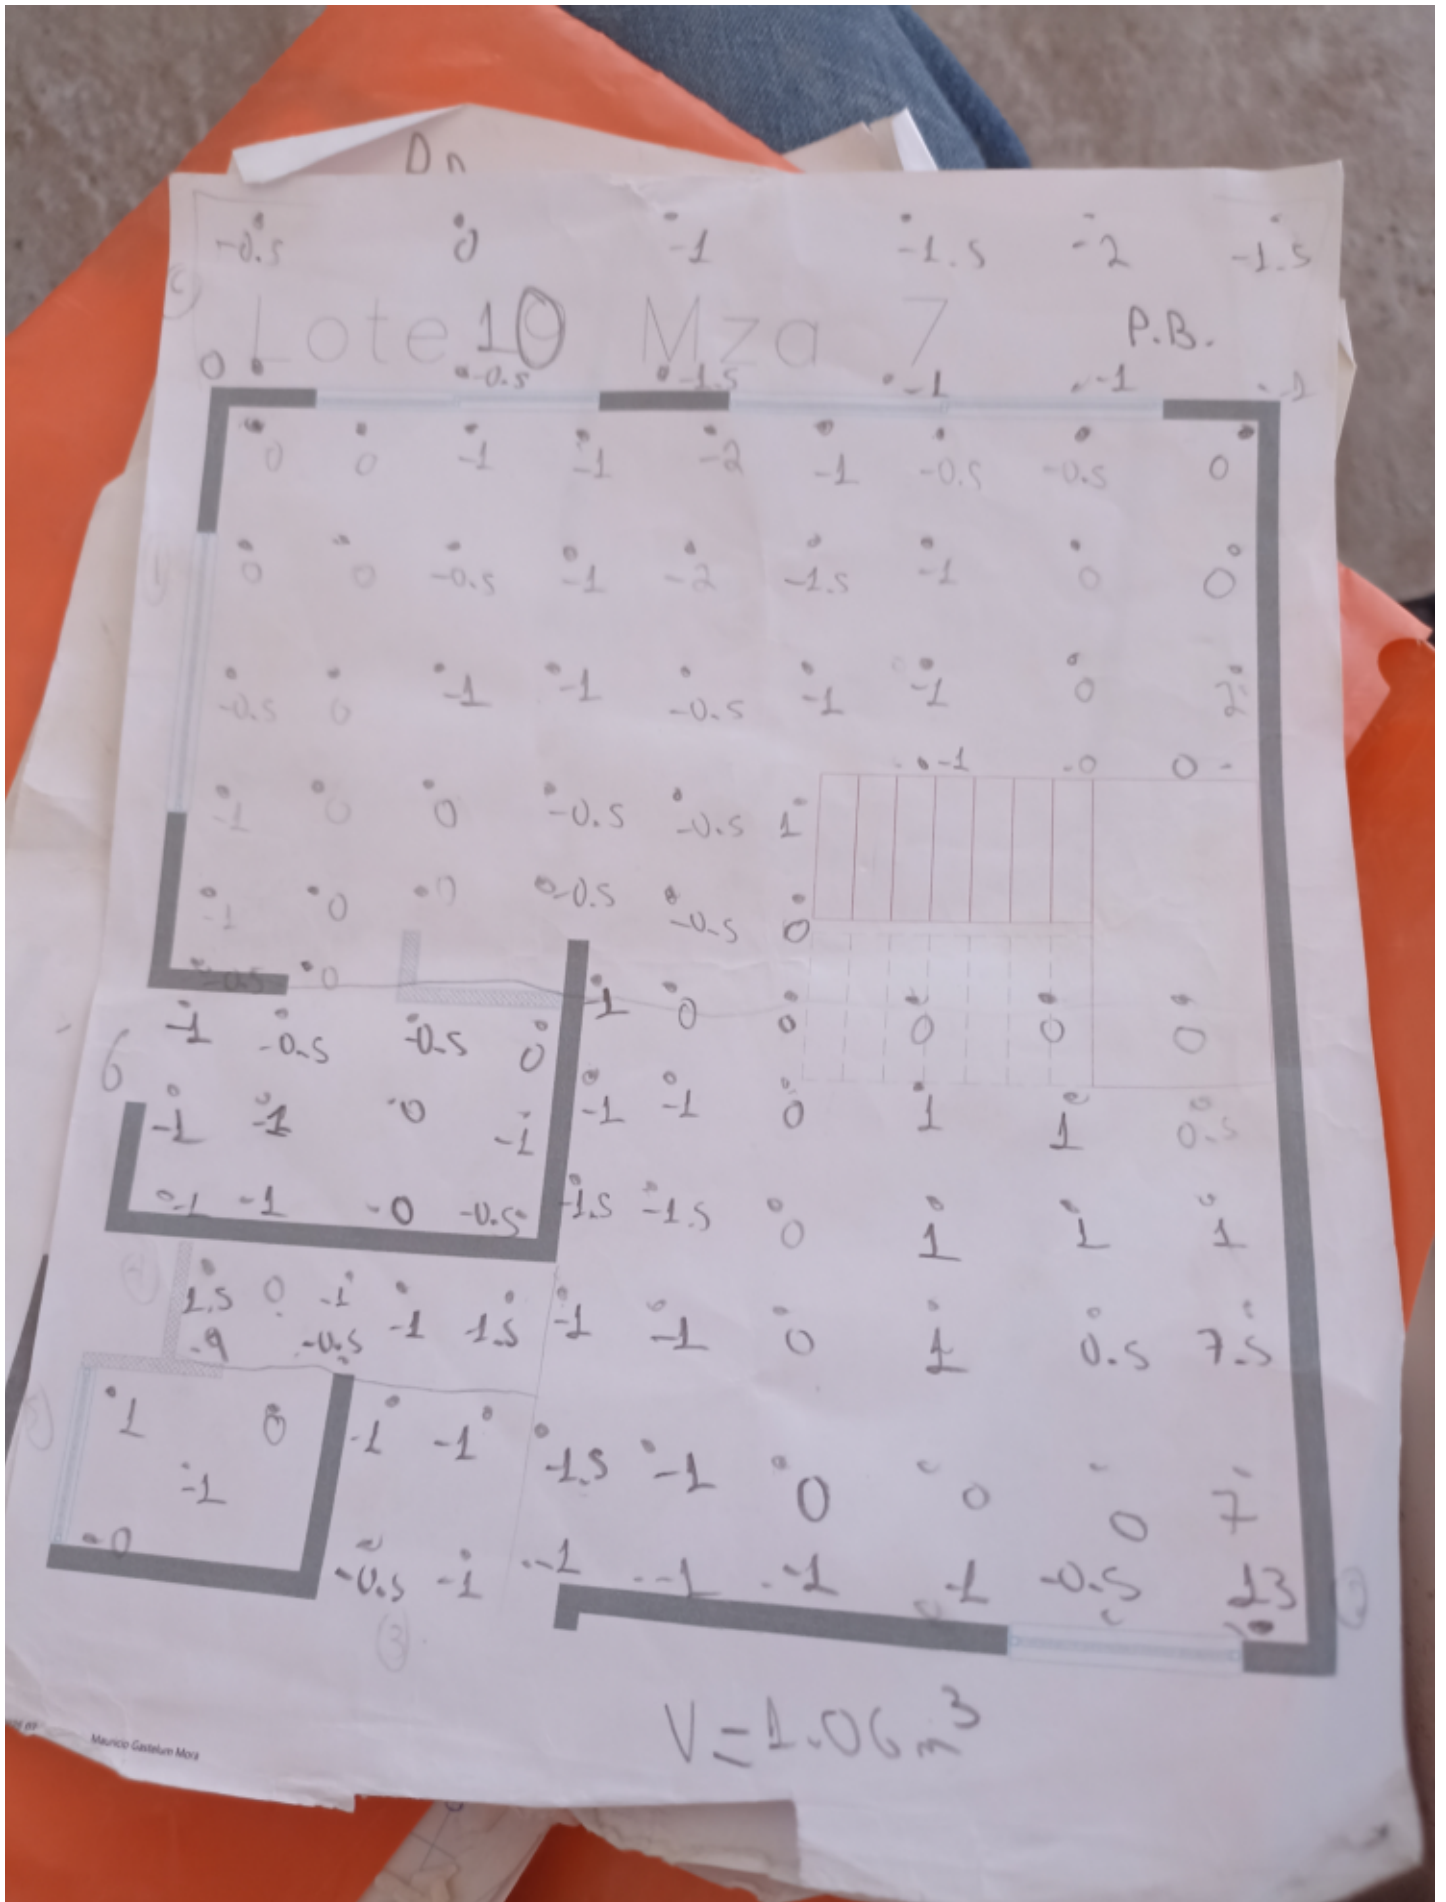

LOTE 10 · MZA 7 (MERLOT) — PLANTA ALTA

Hoja digitalizada · 58.25 m² · prom. 2.50 cm · mortero 1.50 m³ · hoja: V=1.46 m³

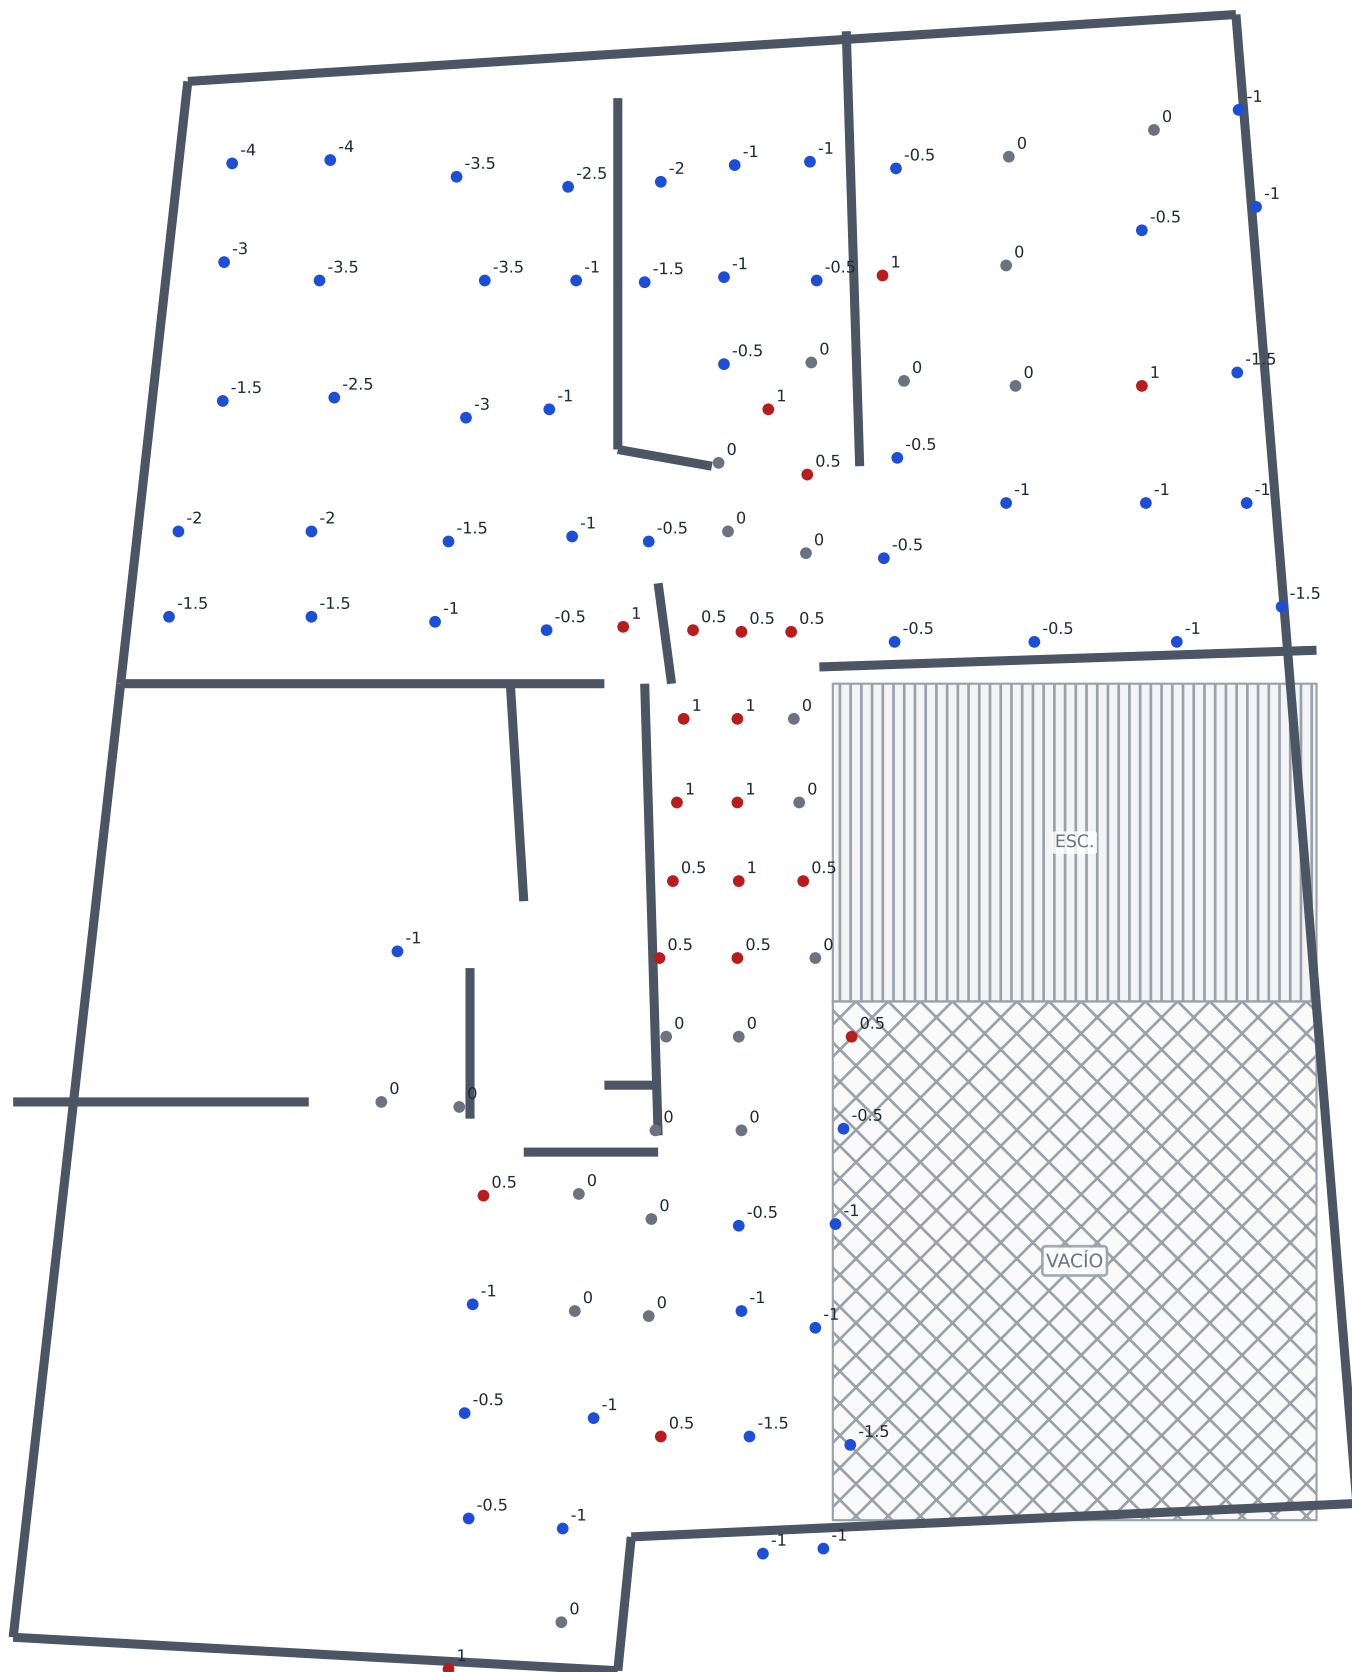

- Relleno (cota negativa: falta nivel)
- Corte (cota positiva: sobra)
- A nivel (0)
- ▨ Vacío / losa sin colar
- ▨ Escalera

