

VIÑAS NORTE

Renivelación — Lote 9, Manzana 7

Merlot

Levantamiento de niveles de losa (renivelación) previo a la colocación de piso.
Se miden cotas en una malla de puntos; el promedio de desnivel define el espesor
de mortero premezclado y su volumen (m^3) por planta.

Convención: cota negativa = falta nivel (RELLENO) · cota positiva = sobra (CORTE).
Cada planta incluye su HOJA DIGITALIZADA y la hoja de campo original.

Fecha: 01/07/2026

Levantó: Mauricio Gastelum Mora

Resumen de renivelación


Lote	Mza	Modelo	Planta	Área m²	Prom. cm	Mortero m³	Estado
L9	M7	Merlot	P.B.	74.86	3.10	2.56	Renivelado (completo)
L9	M7	Merlot	P.A.	58.25	3.40	1.93	Renivelado (completo)
					TOTAL	4.49	

Notas y verificación de hojas de campo

- Verificación foto por foto (encabezado con zoom + aritmética + geometría del plano): f1=L33 P.A. · f2=L33 P.B. · f3=L9 P.B. (V=2.56) · f4=L9 P.A. (V=1.93; la hoja dice 'P.B.' por error) · f5=L10 P.B. (V=1.06) · f6 y f7=MISMA hoja, L10 P.A. (V=1.46).
- L10 M7: P.B. levantada (1.06 m³) pero NO se renivela (prom. 1.2 cm, mínimo). P.A. sí: V hoja 1.46 ≈ 1.5 m³.
- L19 y L17 (Chardonnay): datos dictados del levantamiento; hojas de campo NO incluidas en las fotos recibidas.
- Terrazas (L33/L34 Cabernet, L17 Chardonnay): sin colar; NO entran en la renivelación.
- ⚠ L17 M7 P.A.: 2.59 m³ no cuadra con 2.24 cm × 59.86 m² (≈1.34 m³). Por confirmar; fuera del total.
- L34 M14 (Cabernet): PENDIENTE — se agrega cuando llegue su levantamiento.

LOTE 9 · MZA 7 (MERLOT) — PLANTA BAJA


Hoja digitalizada · 74.86 m² · prom. 3.10 cm · mortero 2.56 m³ · hoja: V=2.56 m3

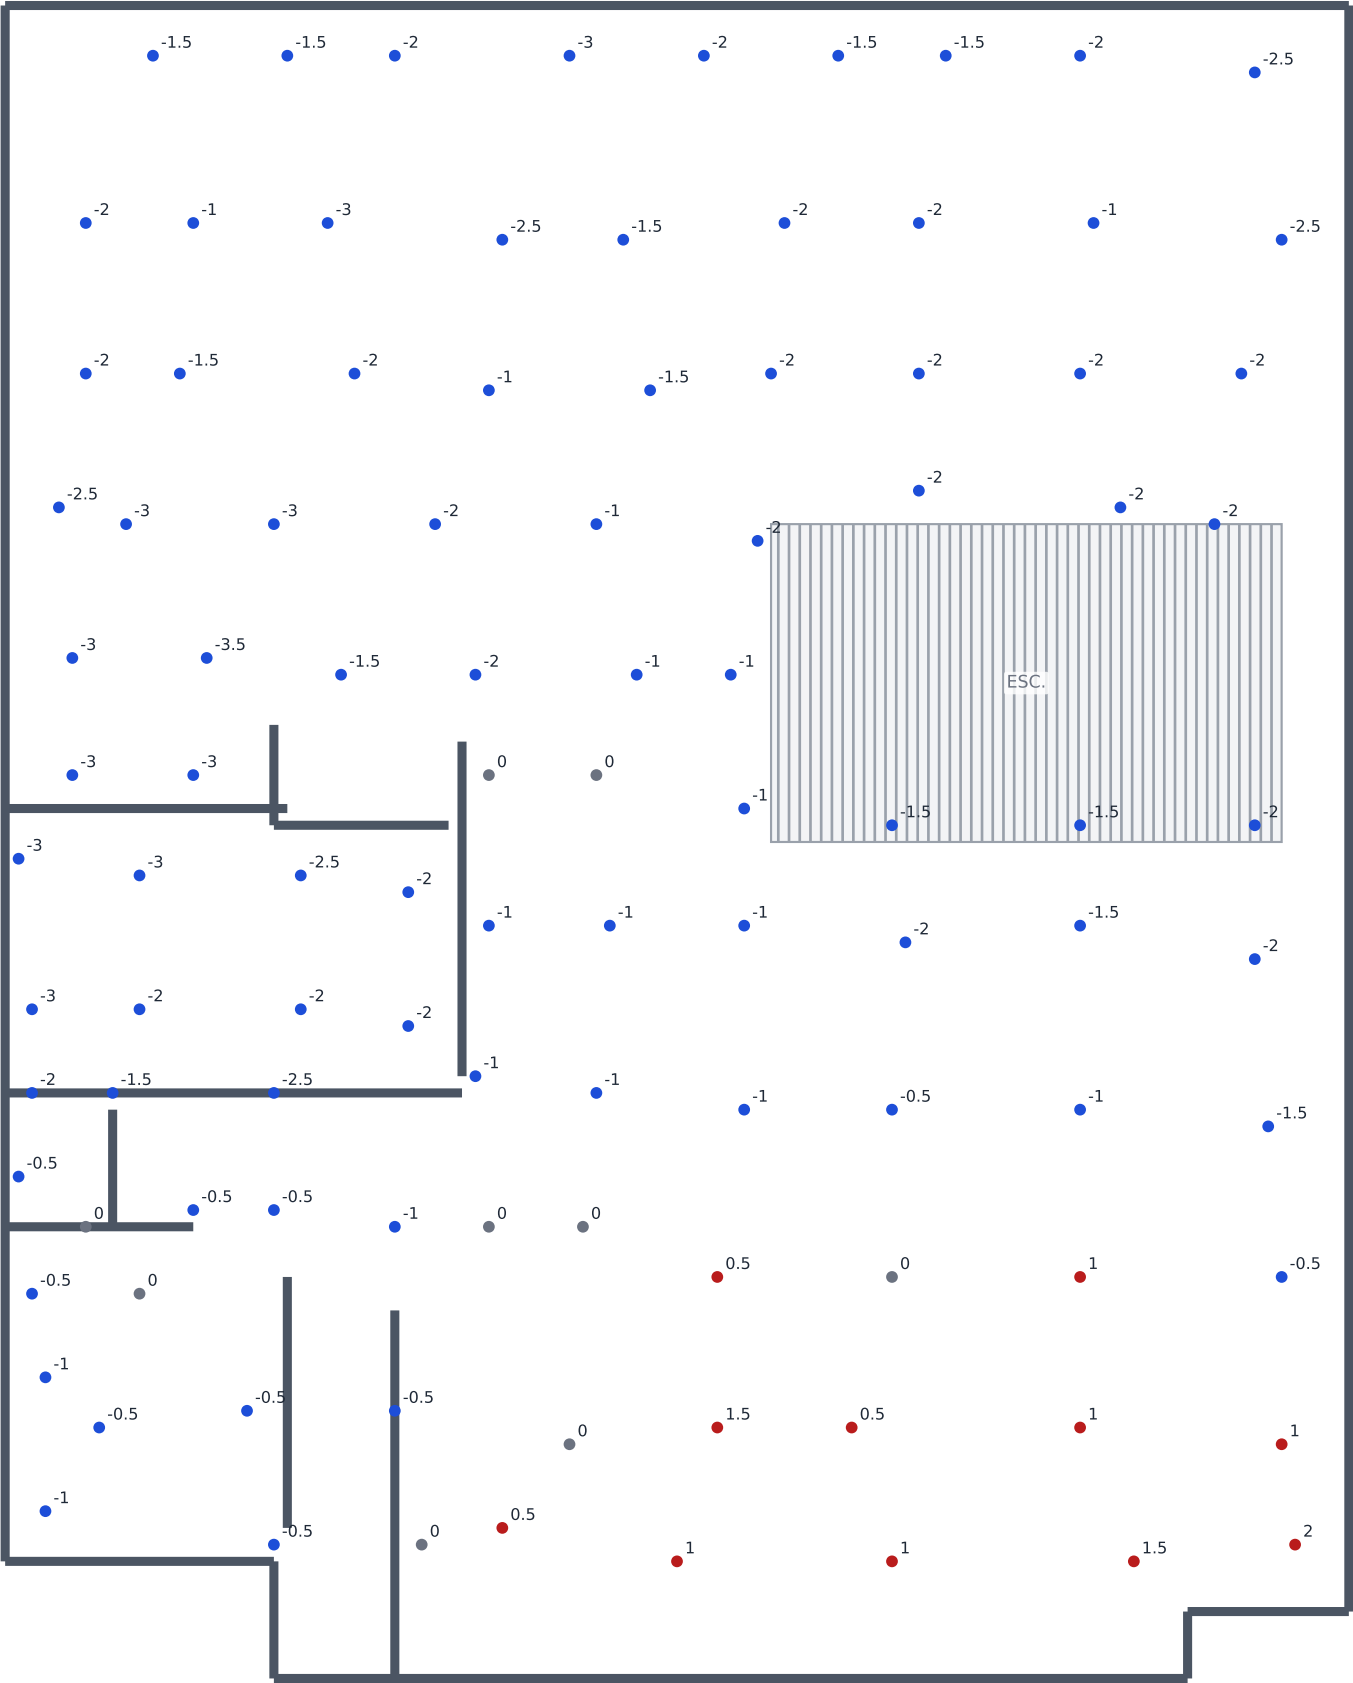

- Relleno (cota negativa: falta nivel)
- A nivel (0)
- ▨


 Vacío / losa sin colar
- Corte (cota positiva: sobra)
- ▨

 Escalera

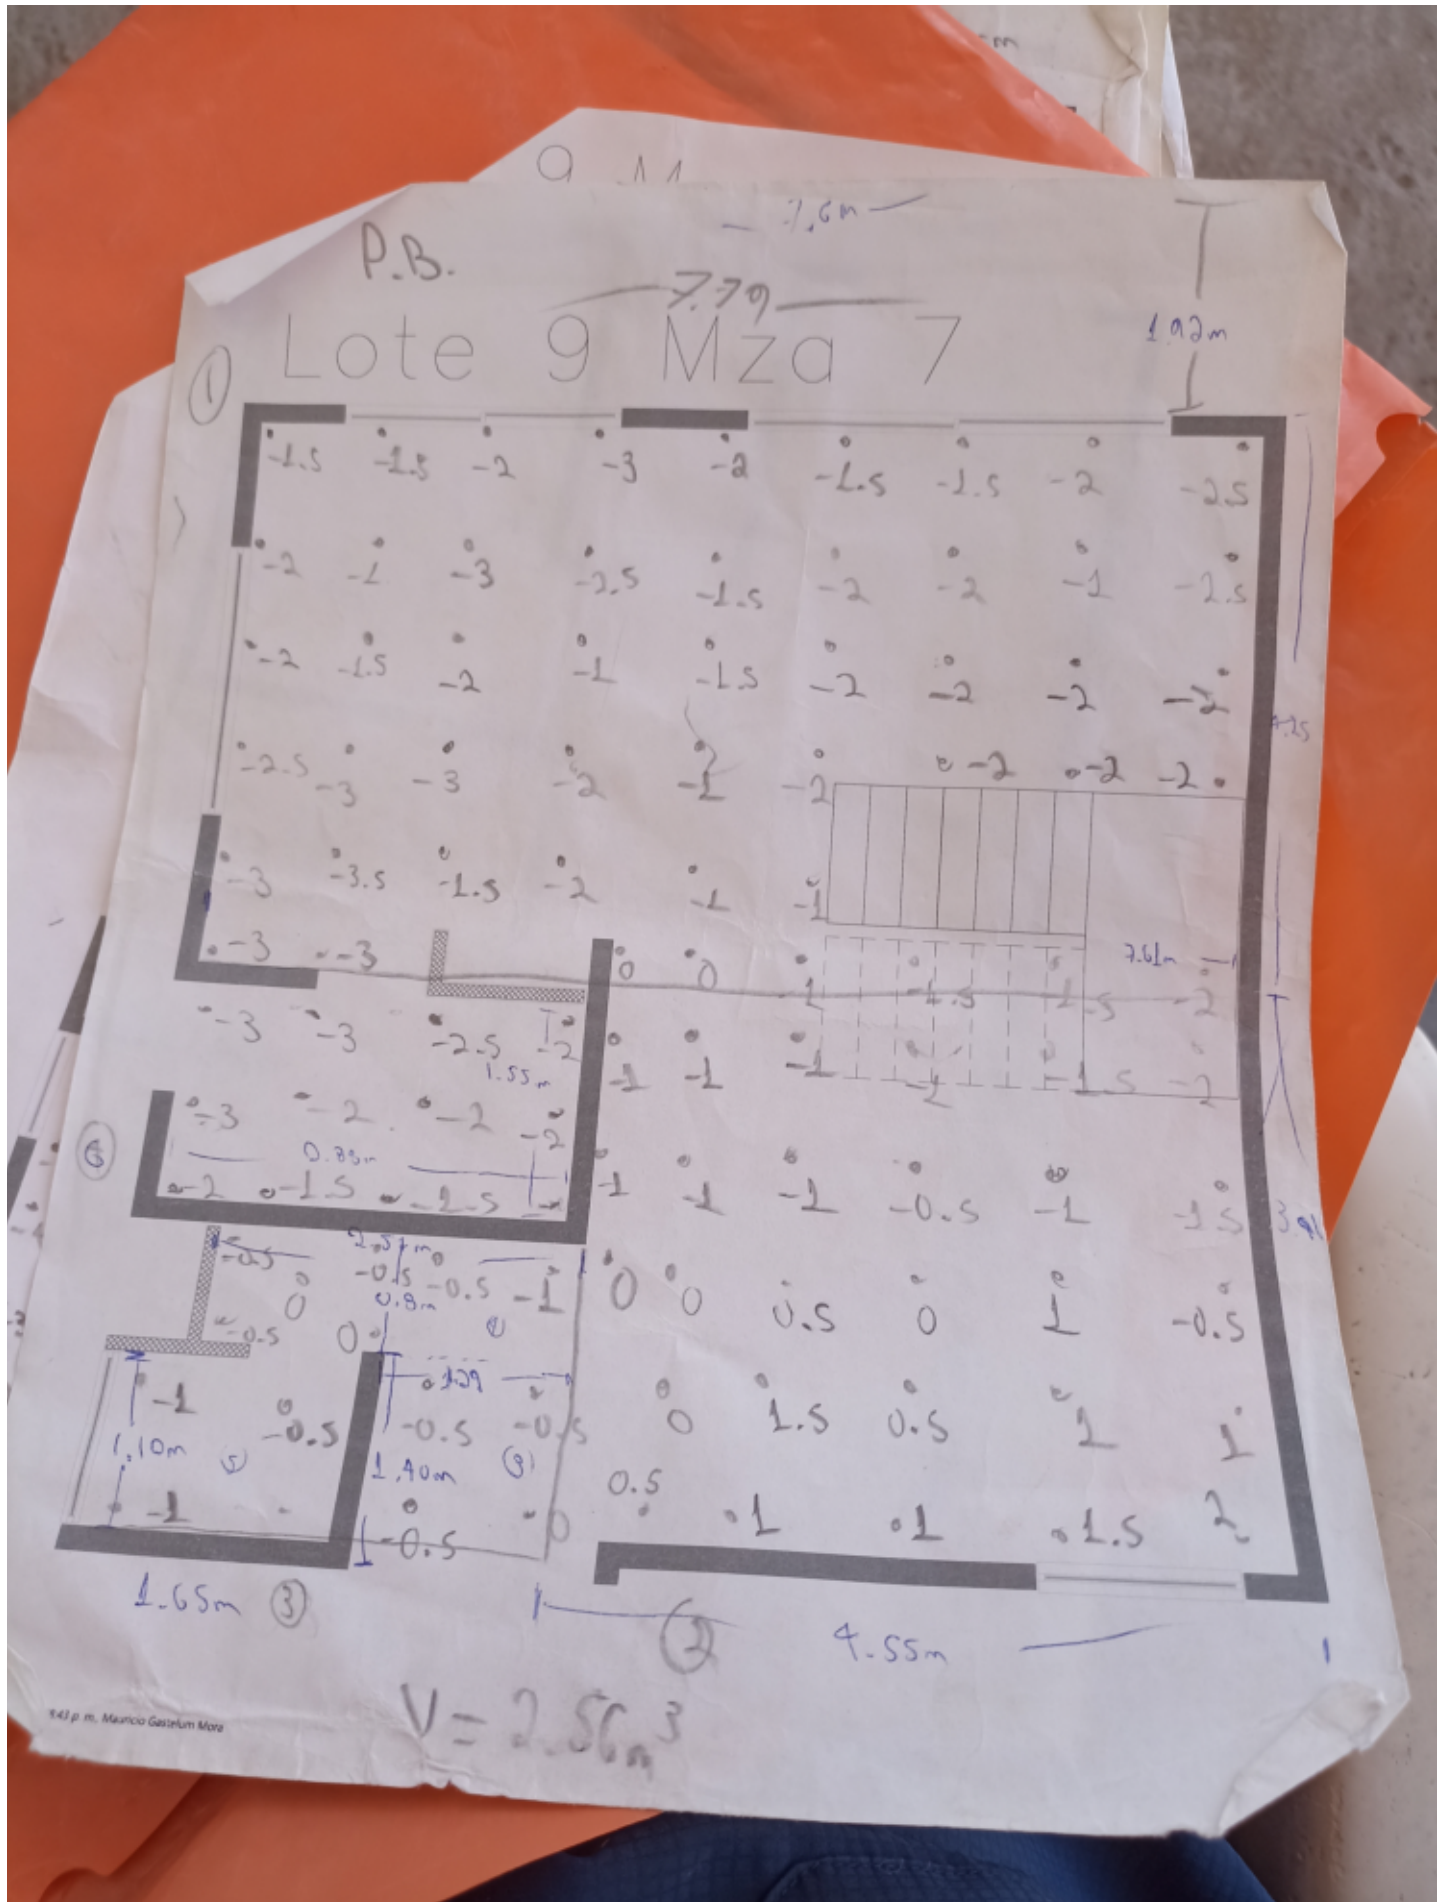

LOTE 9 · MZA 7 (MERLOT) — PLANTA ALTA

Hoja digitalizada · 58.25 m² · prom. 3.40 cm · mortero 1.93 m³ · hoja: V=1.93 m³

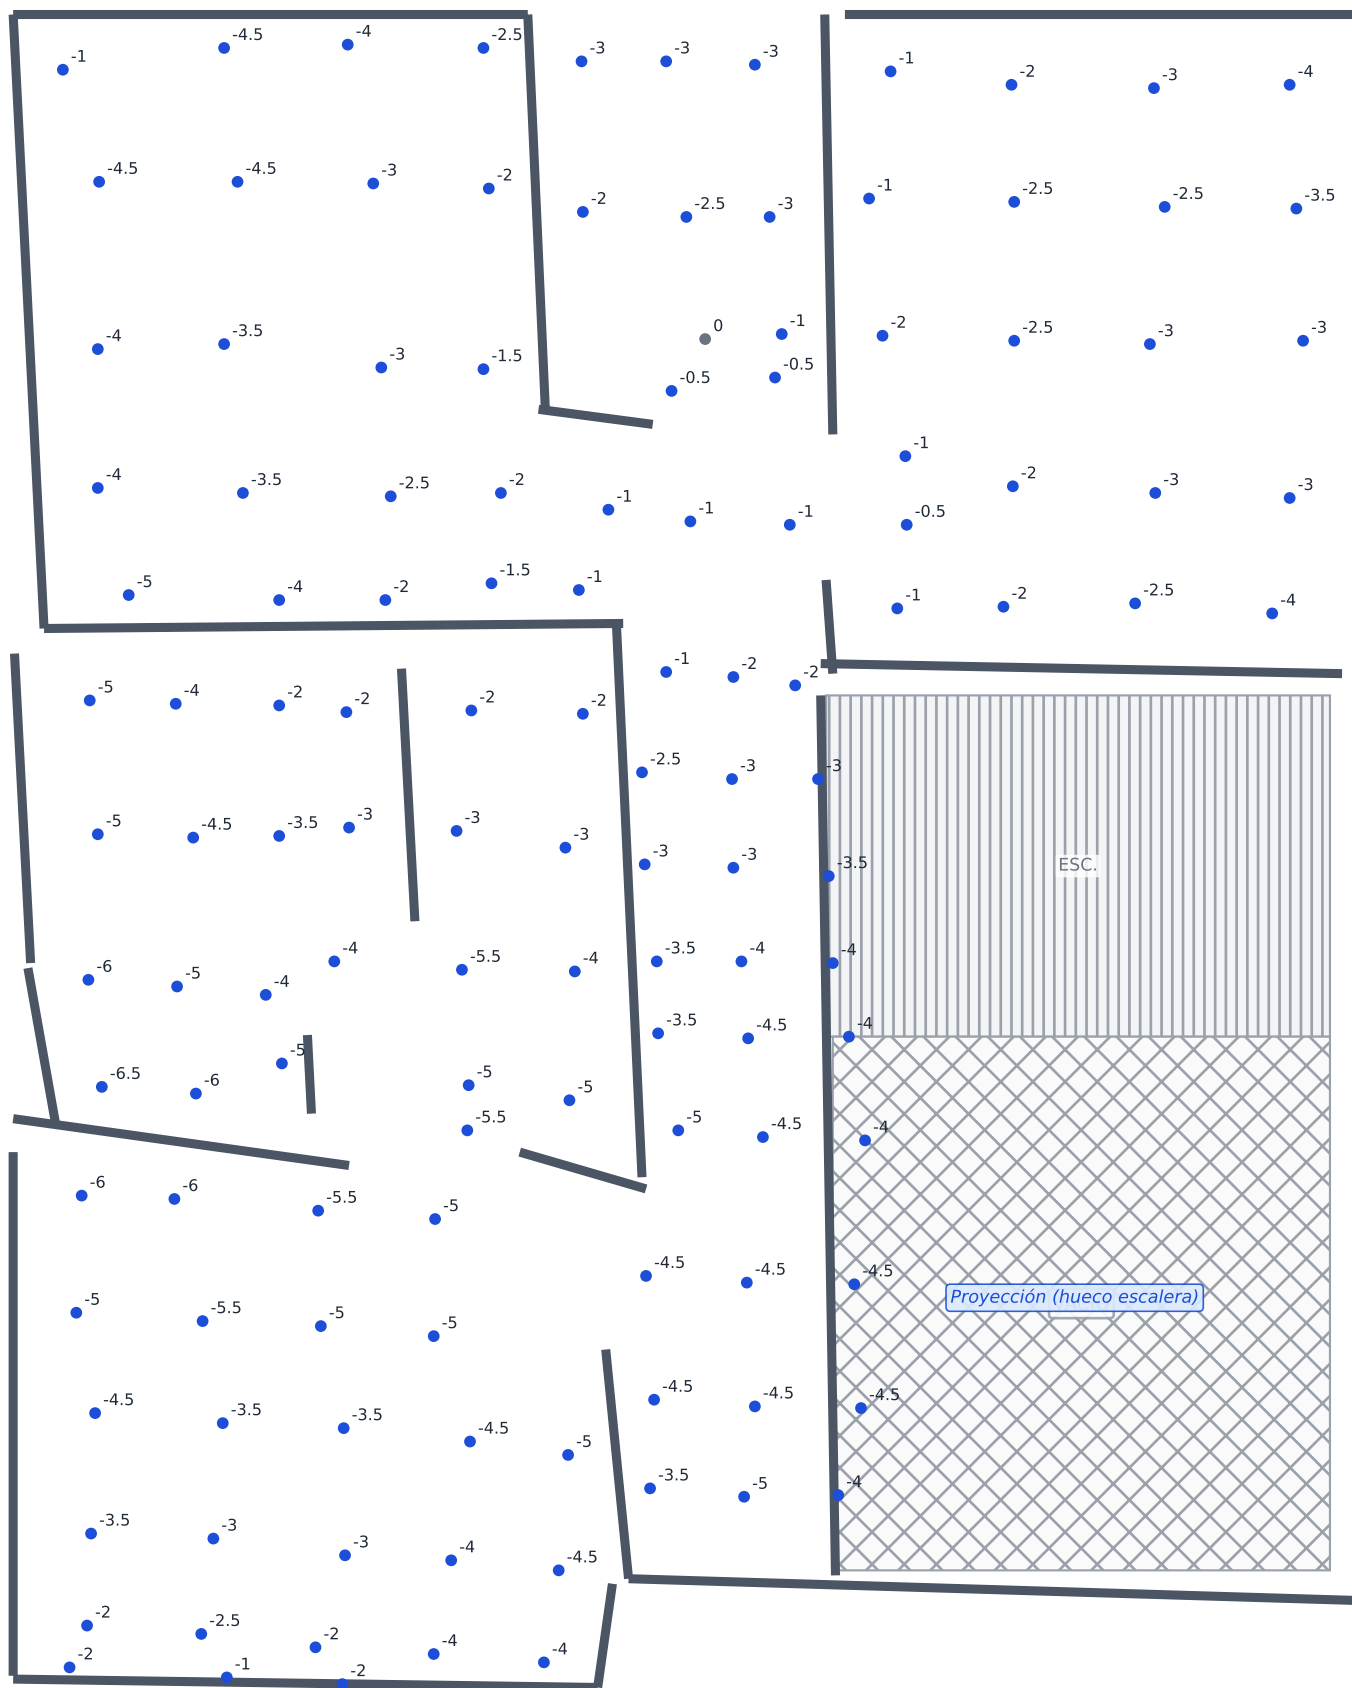

- Relleno (cota negativa: falta nivel)
- A nivel (0)
- Vacío / losa sin colar
- Corte (cota positiva: sobra)
- Escalera

