

VIÑAS NORTE

Renivelación — Lote 33, Manzana 14

Cabernet

Levantamiento de niveles de losa (renivelación) previo a la colocación de piso.
Cotas medidas en malla de puntos; el promedio define el espesor de mortero
premezclado y su volumen (m^3) por planta.

Convención: cota negativa = falta nivel (RELLENO) · cota positiva = sobra (CORTE).
Hojas digitalizadas con la GEOMETRÍA EXACTA de muros del despiece (DWG),
en la misma orientación que la hoja de campo.

Fecha: 01/07/2026

Levantó: Mauricio Gastelum Mora

Resumen de renivelación


Lote	Mza	Modelo	Planta	Área m²	Prom. cm	Mortero m³	Estado
L33	M14	Cabernet	P.B.	72.63	1.84	1.34	Renivelado
L33	M14	Cabernet	P.A.	65.21	2.94	1.88	Renivelado
					TOTAL	3.22	

Notas y verificación de hojas de campo

- Verificación foto por foto (zoom + aritmética + geometría): f1=L33 P.A. · f2=L33 P.B. · f3=L9 P.B. (V=2.56) · f4=L9 P.A. (V=1.93; hoja dice 'P.B.' por error) · f5=L10 P.B. (V=1.06) · f6=f7=misma hoja, L10 P.A. (V=1.46).
- L10 M7: P.B. levantada (1.06 m³) pero NO se renivela (prom. 1.2 cm). P.A. sí: 1.46 ≈ 1.5 m³.
- L19 y L17 (Chardonnay): datos dictados; hojas de campo no incluidas en las fotos.
- Terrazas (L33/L34 Cabernet, L17 Chardonnay): sin colar; NO entran en la renivelación.
- ⚠ L17 M7 P.A.: 2.59 m³ no cuadra con 2.24 cm × 59.86 m² (≈1.34 m³). Por confirmar; fuera del total.
- L34 M14 (Cabernet): PENDIENTE — se agrega cuando llegue su levantamiento.


LOTE 33 · MZA 14 (CABERNET) — PLANTA BAJA

Hoja digitalizada · 72.63 m² · prom. 1.84 cm · mortero 1.34 m³

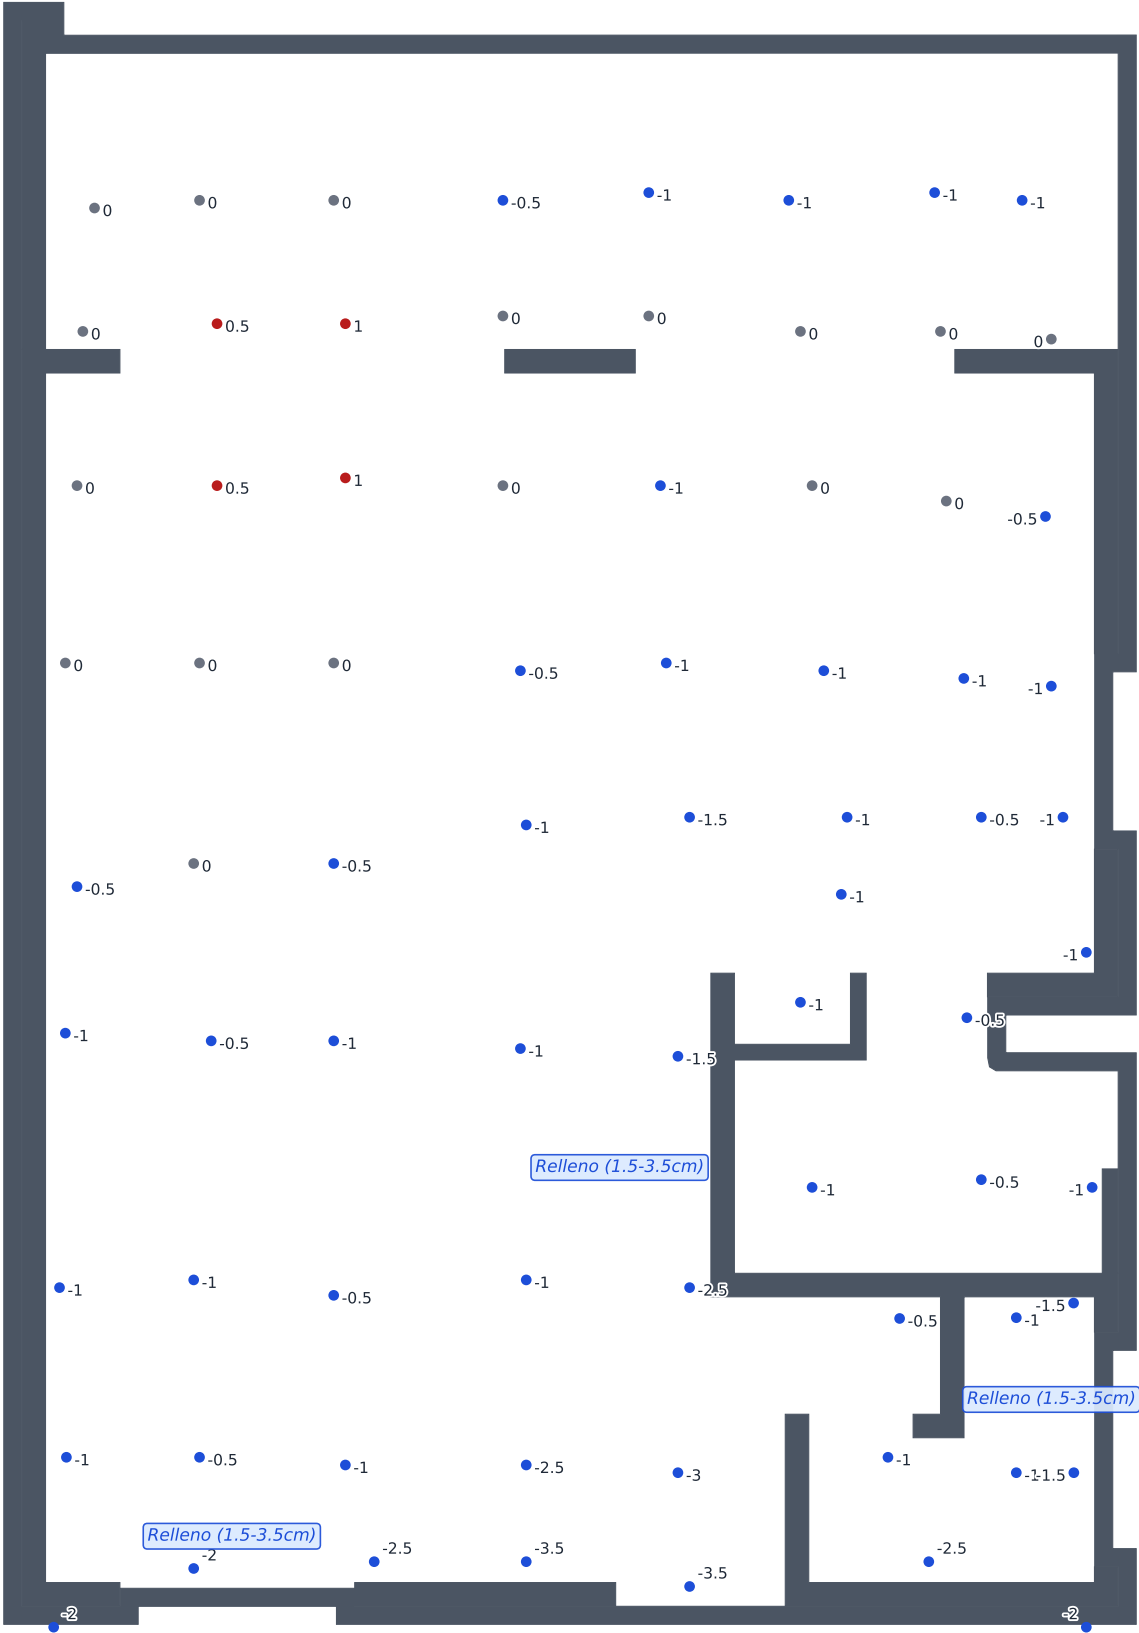


● Relleno (cota -) ● Corte (cota +) ● A nivel (0)

Hoja de campo original

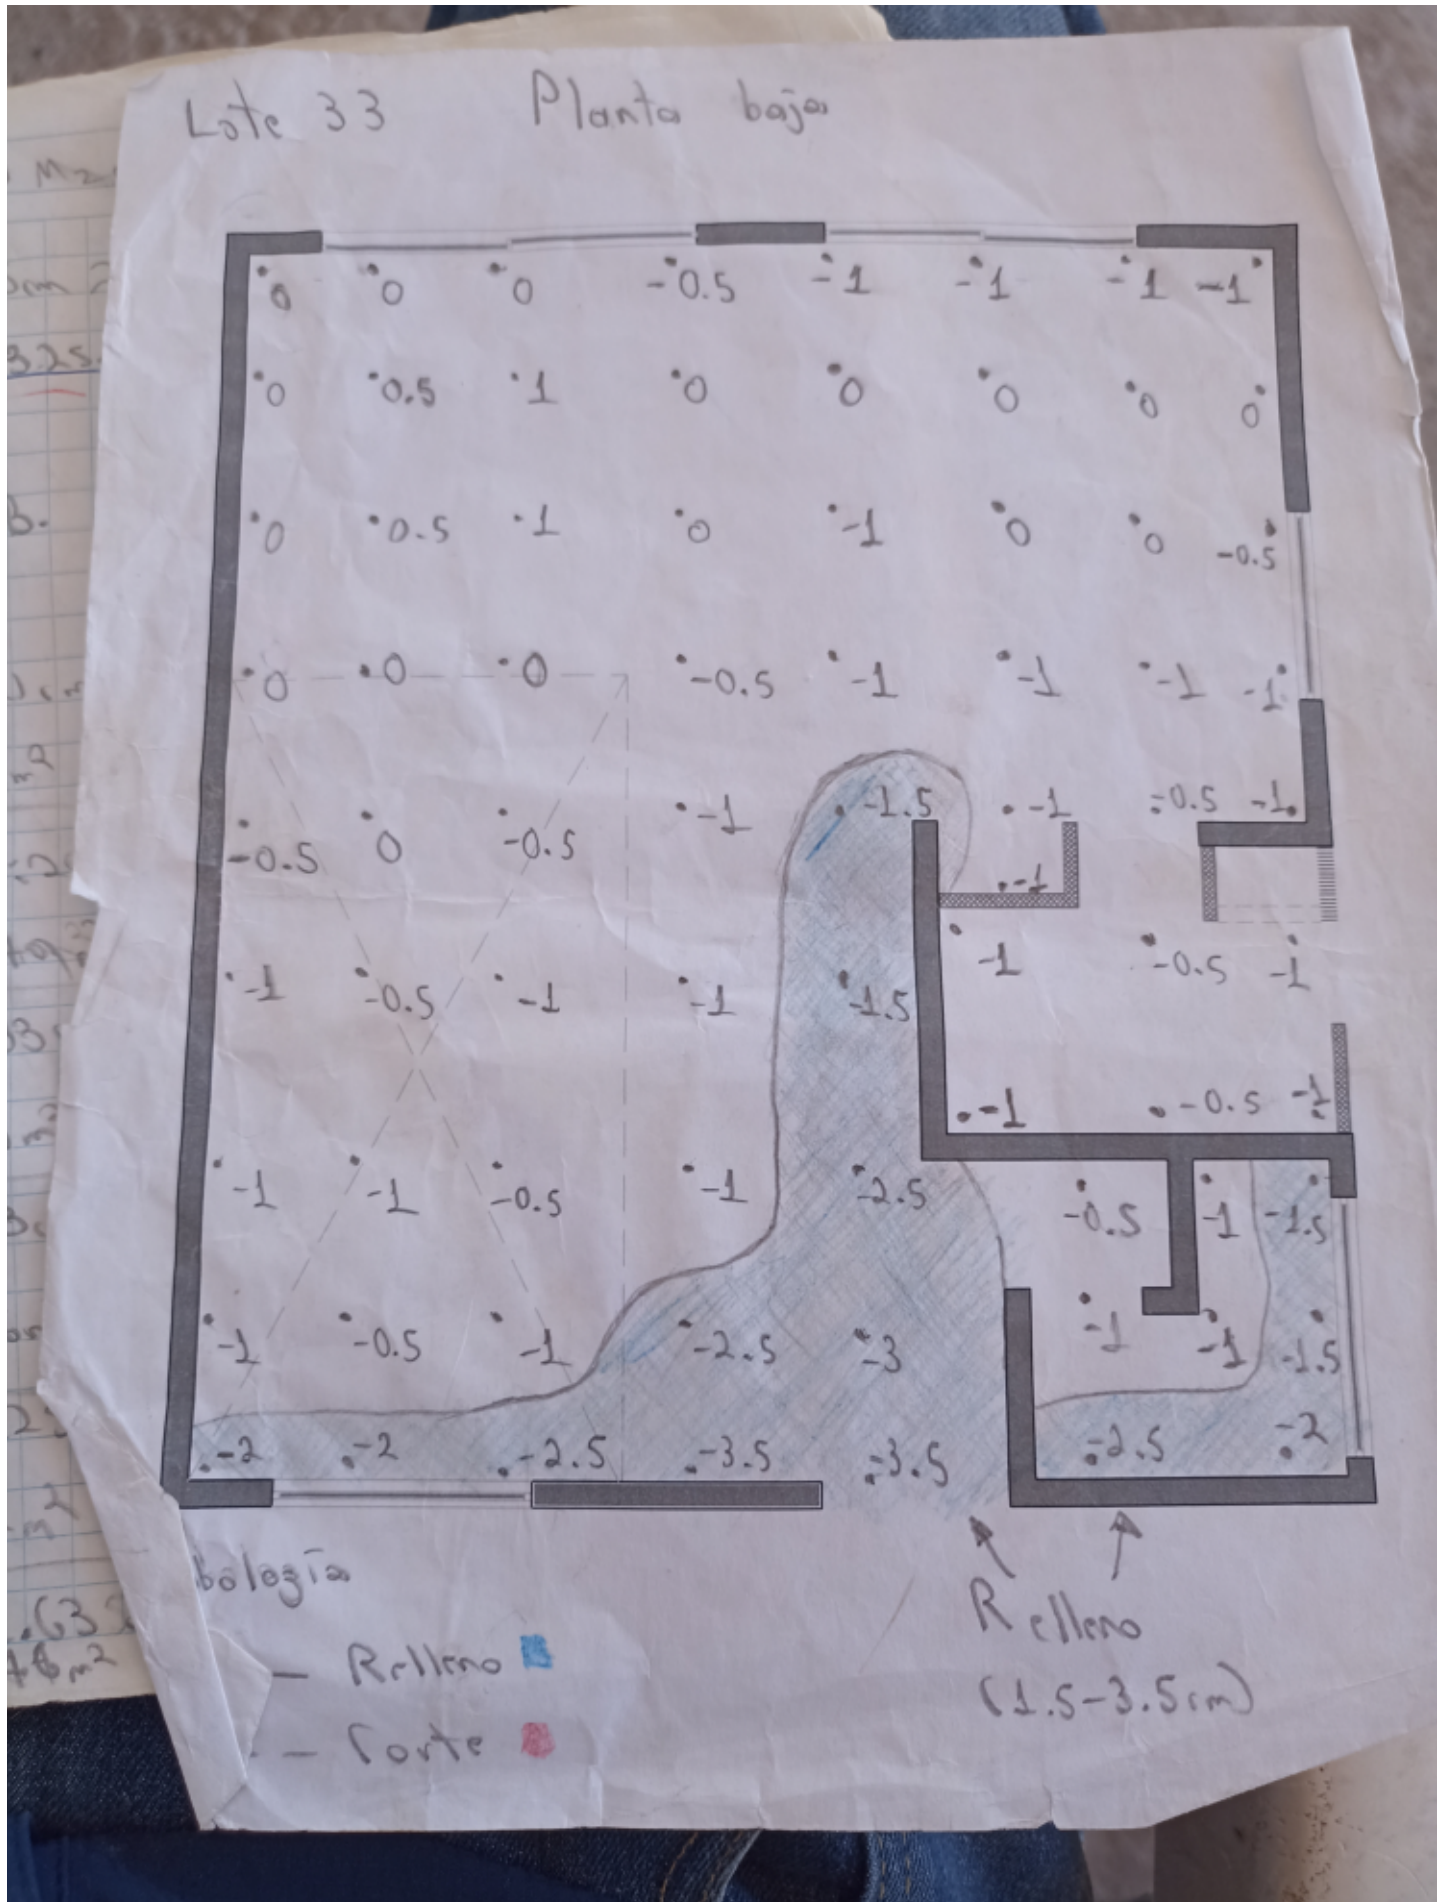

LOTE 33 · MZA 14 (CABERNET) — PLANTA ALTA

Hoja digitalizada · 65.21 m² · prom. 2.94 cm · mortero 1.88 m³

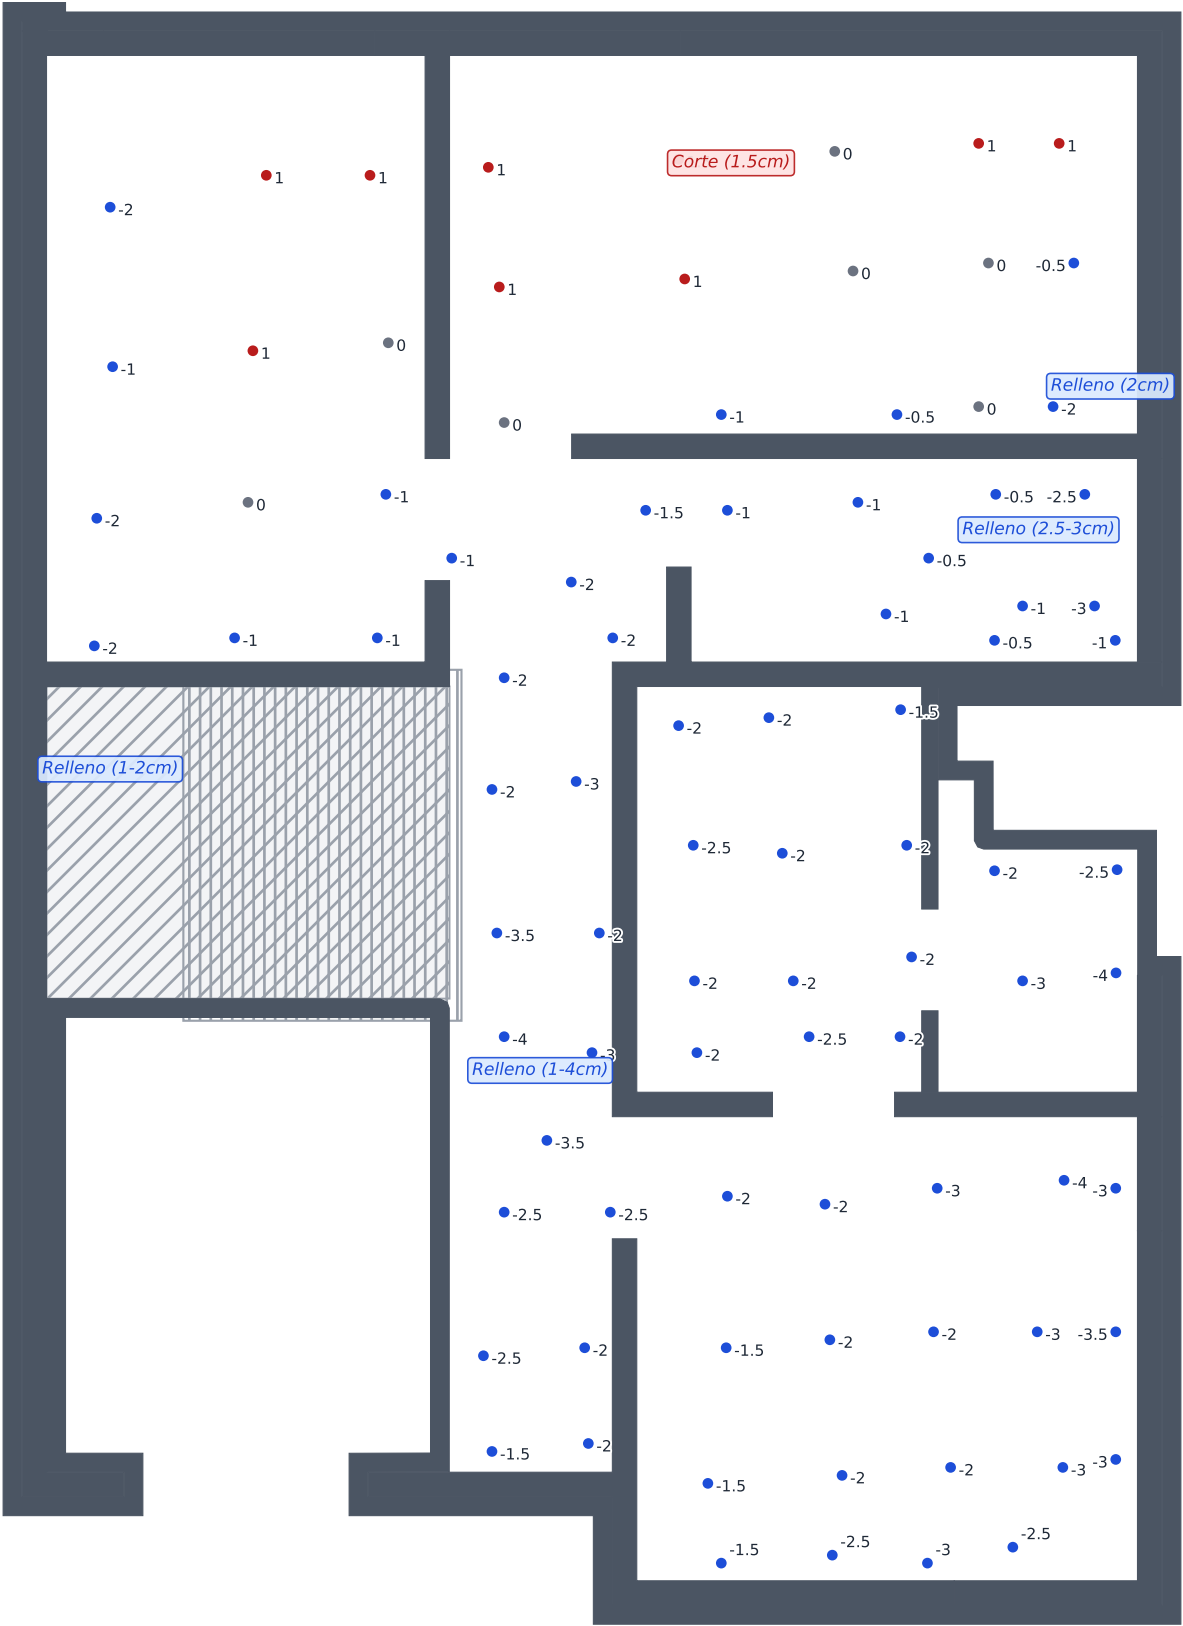

● Relleno (cota -) ● Corte (cota +) ● A nivel (0) ▨ Escalera (hueco)

