

VIÑAS NORTE

Renivelación de Losas — Resumen General

Manzana 7 y Manzana 14 · hojas digitalizadas con muros exactos

Levantamiento de niveles de losa (renivelación) previo a la colocación de piso.
Cotas medidas en malla de puntos; el promedio define el espesor de mortero
premezclado y su volumen (m^3) por planta.

Convención: cota negativa = falta nivel (RELLENO) · cota positiva = sobra (CORTE).
Hojas digitalizadas con la GEOMETRÍA EXACTA de muros del despiece (DWG).

Fecha: 01/07/2026

Levantó: Mauricio Gastelum Mora

Resumen de renivelación


Lote	Mza	Modelo	Planta	Área m²	Prom. cm	Mortero m³	Estado
L33	M14	Cabernet	P.B.	72.63	1.84	1.34	Renivelado
L33	M14	Cabernet	P.A.	65.21	2.94	1.88	Renivelado
L9	M7	Merlot	P.B.	74.86	3.10	2.56	Renivelado
L9	M7	Merlot	P.A.	58.25	3.40	1.93	Renivelado
L10	M7	Merlot	P.B.	74.86	1.20	—	No renivelado
L10	M7	Merlot	P.A.	58.25	2.50	1.50	Renivelado
L19	M7	Chardonnay	P.B.	85.79	1.71	1.46	Por renivelar
L19	M7	Chardonnay	P.A.	59.86	3.40	1.50	Por renivelar
L17	M7	Chardonnay	P.B.	85.79	1.45	1.28	Por renivelar
L17	M7	Chardonnay	P.A.	59.86	2.24	2.59	Por renivelar
						9.21	TOTAL EJECUTADO
						6.83	TOTAL POR RENIVELAR

Notas y verificación


- Color de fila = lote · color de la celda Estado: verde=renivelado, ámbar=no renivelado, azul=por renivelar.
- Verificación foto por foto (zoom + aritmética + geometría): f1=L33 P.A. · f2=L33 P.B. · f3=L9 P.B. (V=2.56) · f4=L9 P.A. (V=1.93; hoja dice 'P.B.' por error) · f5=L10 P.B. (V=1.06) · f6=f7=misma hoja, L10 P.A. (V=1.46).
 - L10 M7: P.B. levantada (1.06 m³) pero NO se renivela (prom. 1.2 cm). P.A. renivelada (1.46 ≈ 1.5 m³). Planos de L10 espejados para coincidir con la casa en campo.
 - L19 M7 y L17 M7 (Chardonnay): levantamientos DIGITALIZADOS (hojas del 2 de julio); POR RENIVELAR — L19 en proceso hoy jueves 2 de julio, L17 sin fecha. Referencias de hoja: L19 P.A. –3 cm, L19 P.B. –2 cm, L17 P.A. –3 cm.
 - Terrazas (no coladas): fuera de la renivelación.
 - ⚠ L17 M7 P.A.: 2.59 m³ no cuadra con 2.24 cm × 59.86 m² (≈1.34 m³). Confirmar antes de pedir mortero.

LOTE 33 · MZA 14 (CABERNET) — PLANTA BAJA

Hoja digitalizada · 72.63 m² · prom. 1.84 cm · mortero 1.34 m³

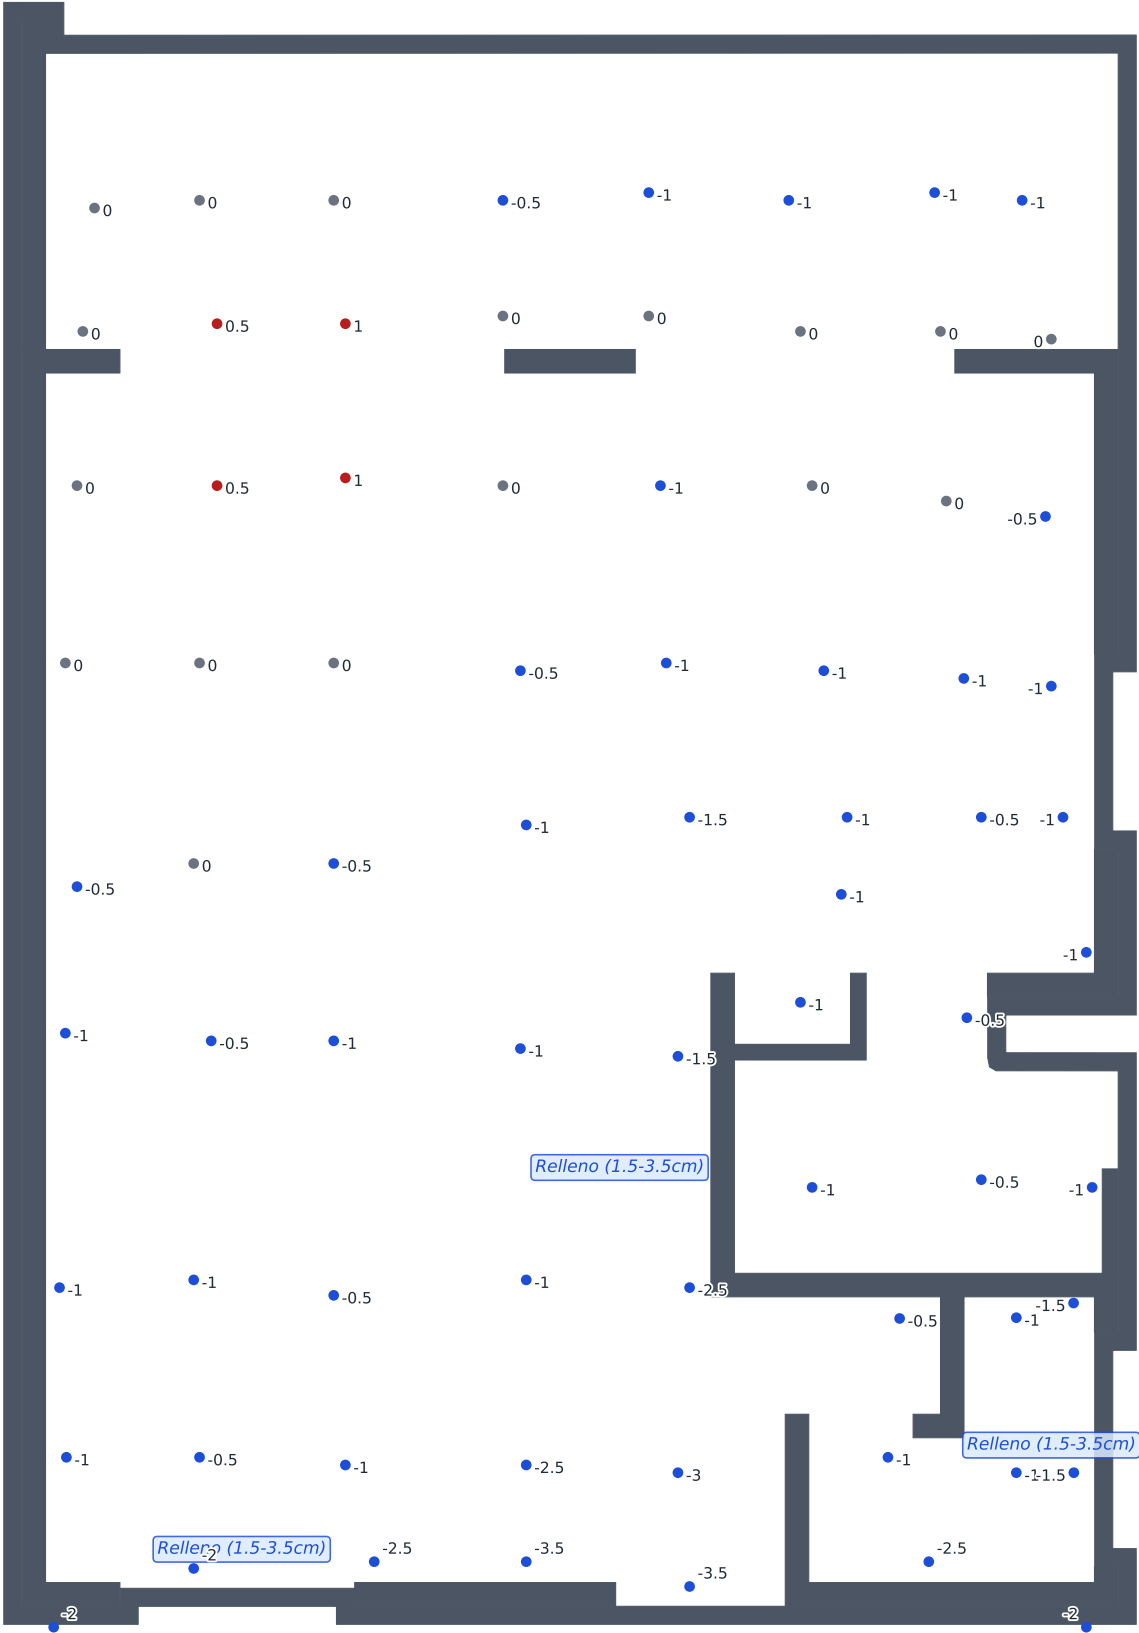


Hoja de campo original

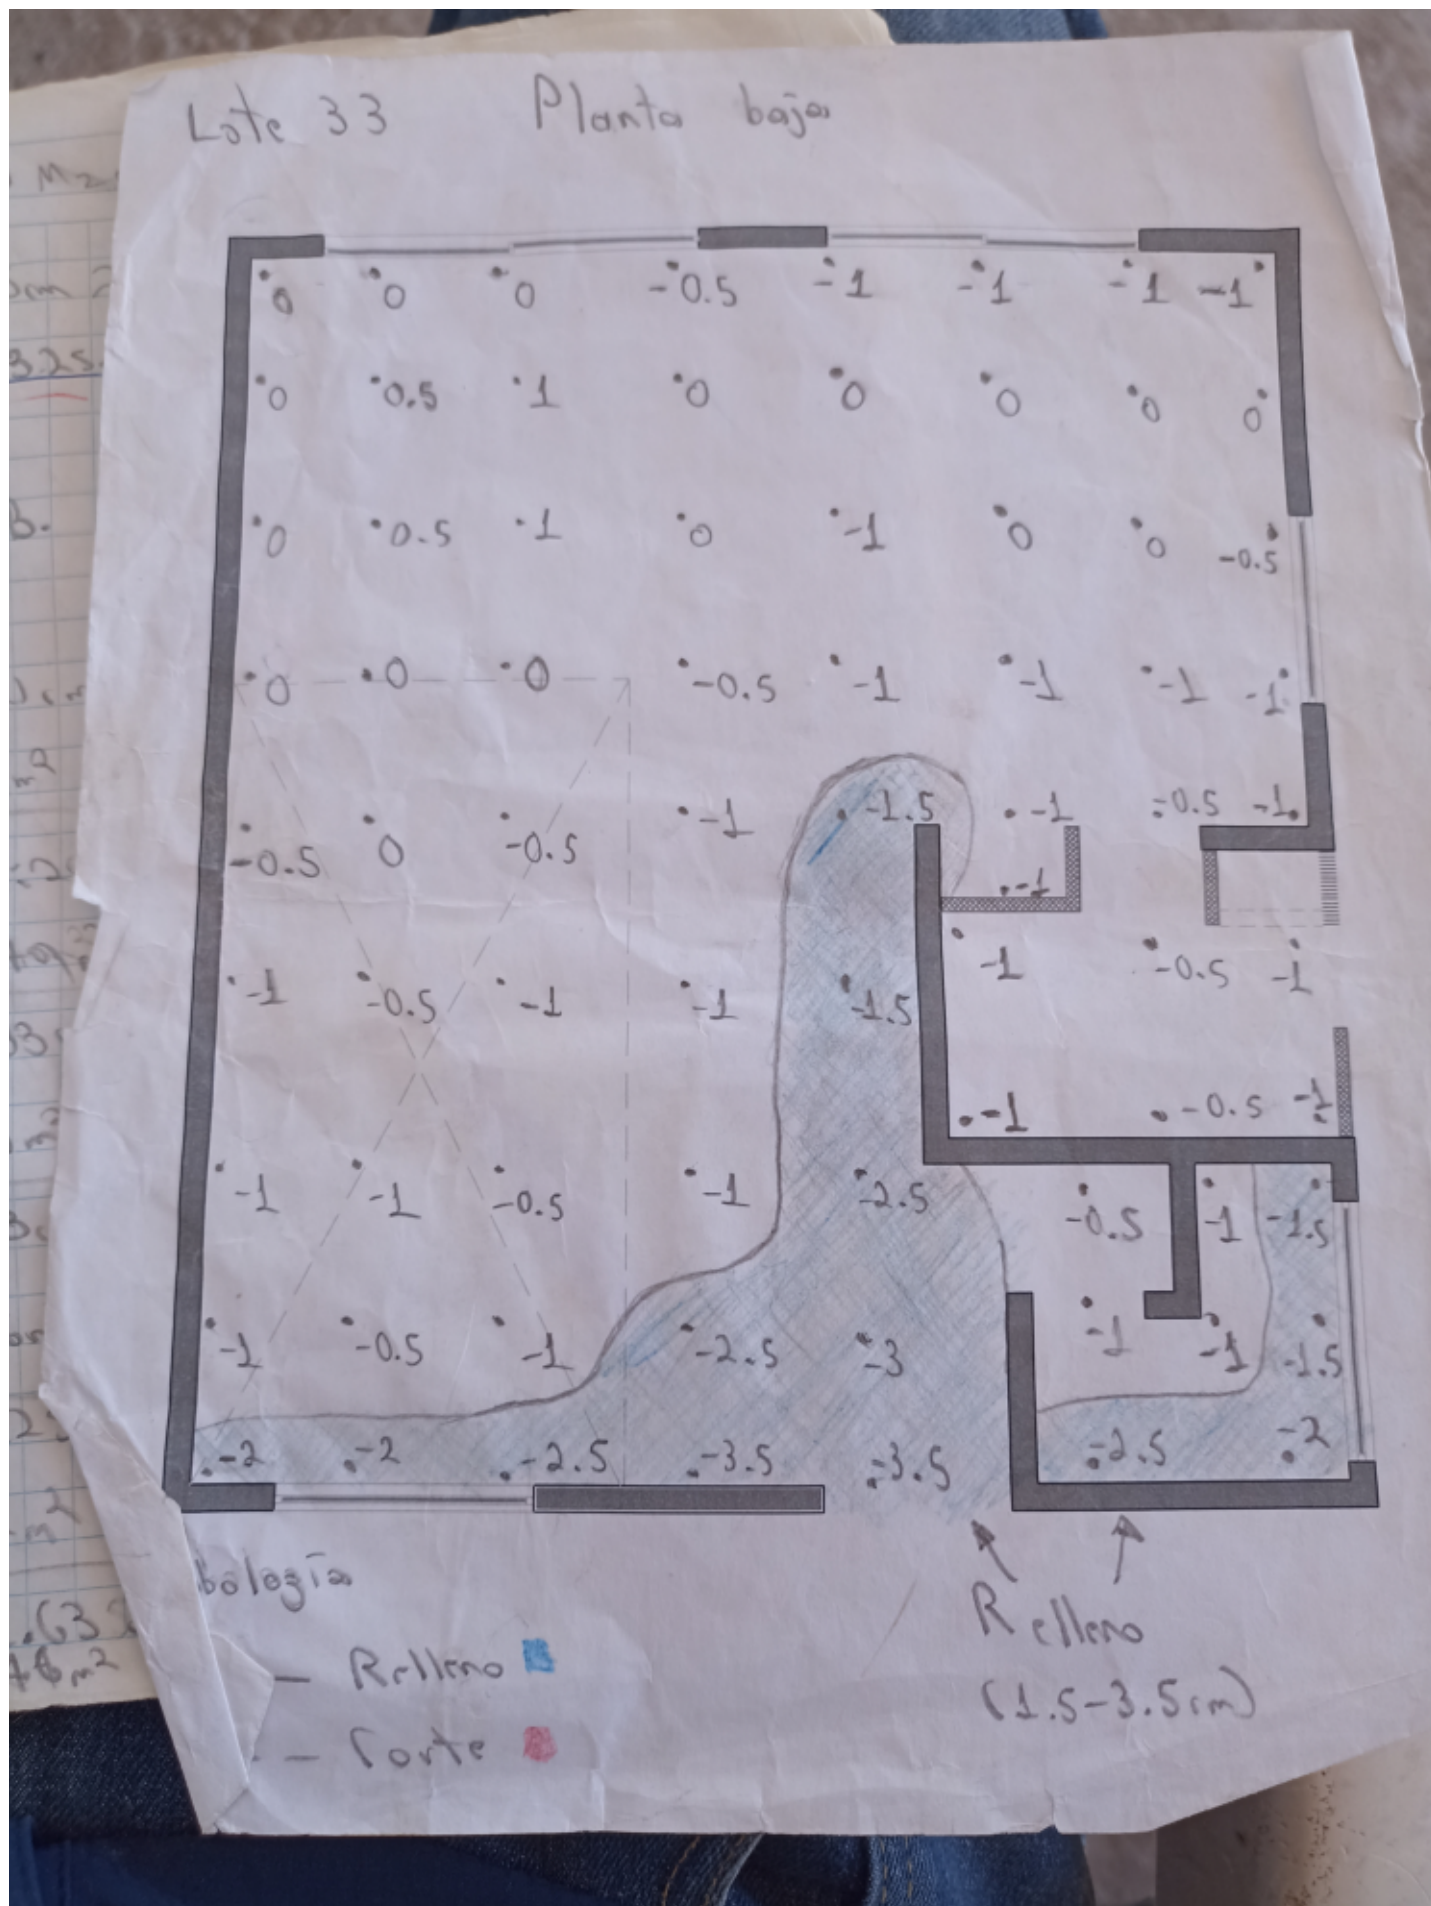


LOTE 33 · MZA 14 (CABERNET) — PLANTA ALTA

Hoja digitalizada · 65.21 m² · prom. 2.94 cm · mortero 1.88 m³

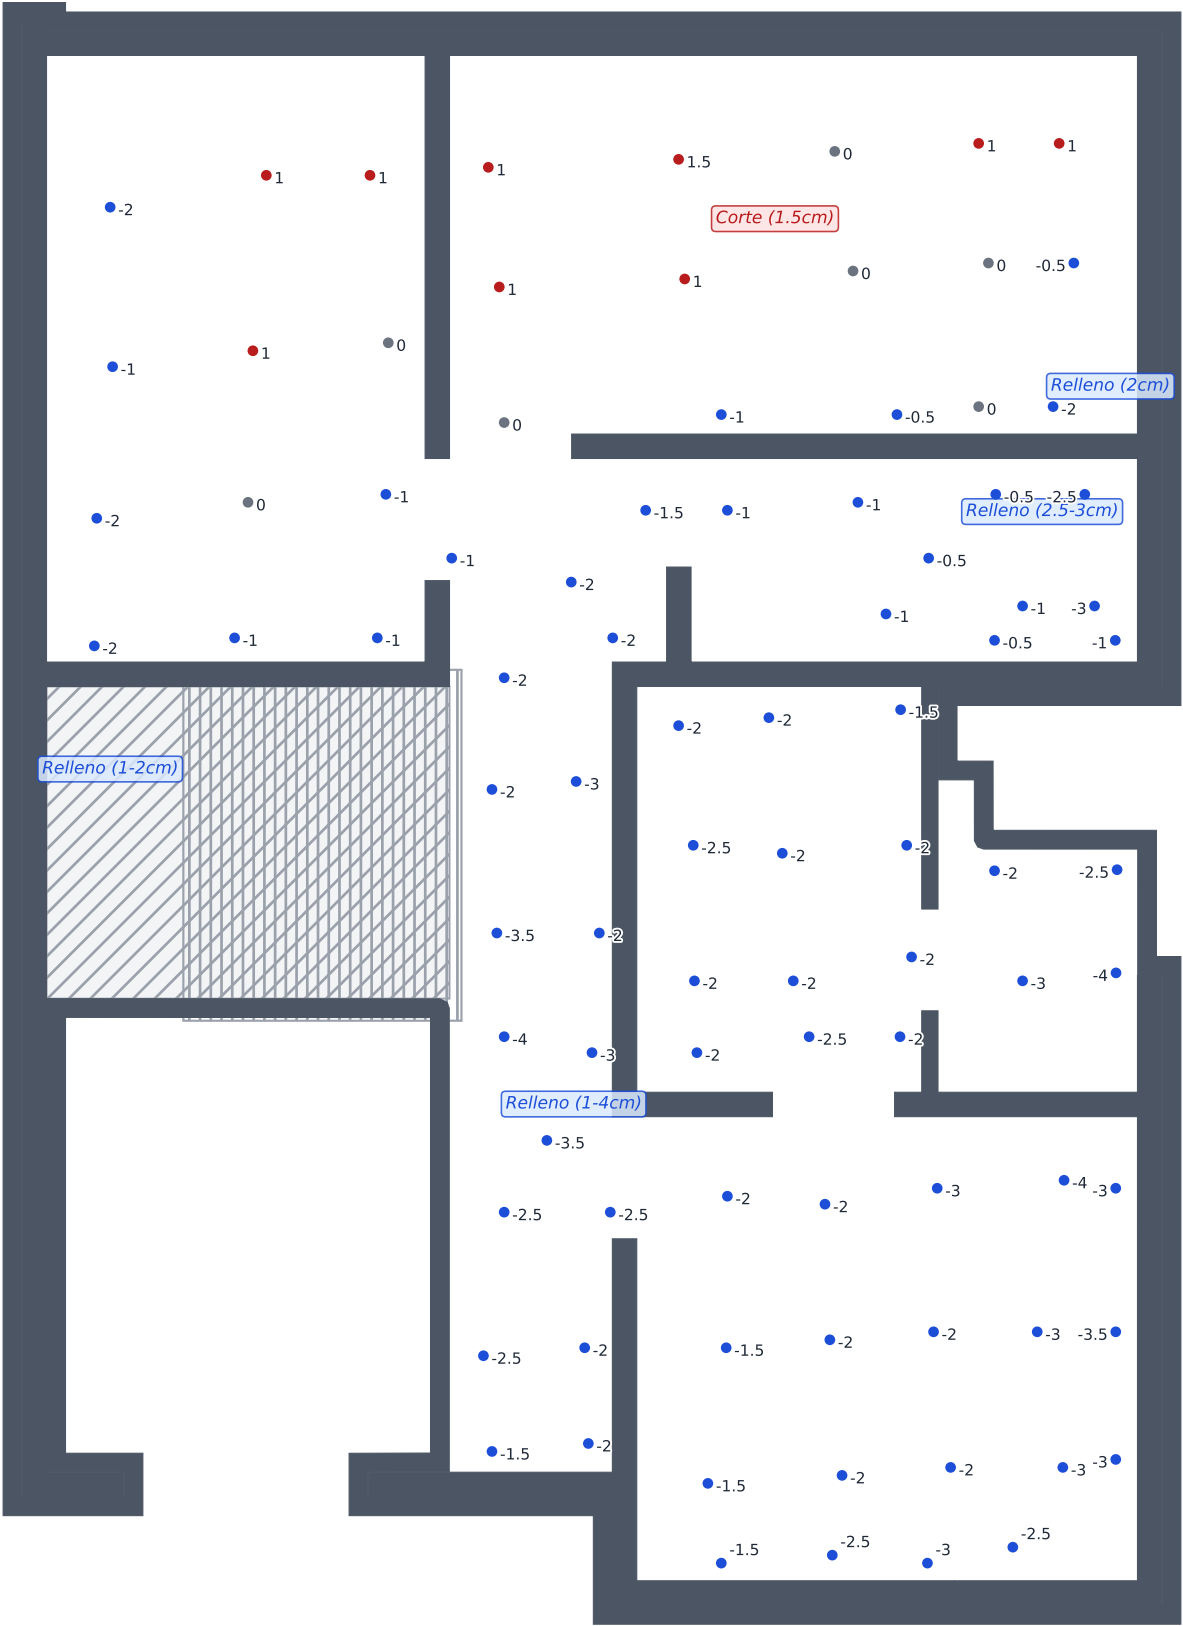

● Relleno (cota -) ● Corte (cota +) ● A nivel (0) ▨ Escalera (hueco)

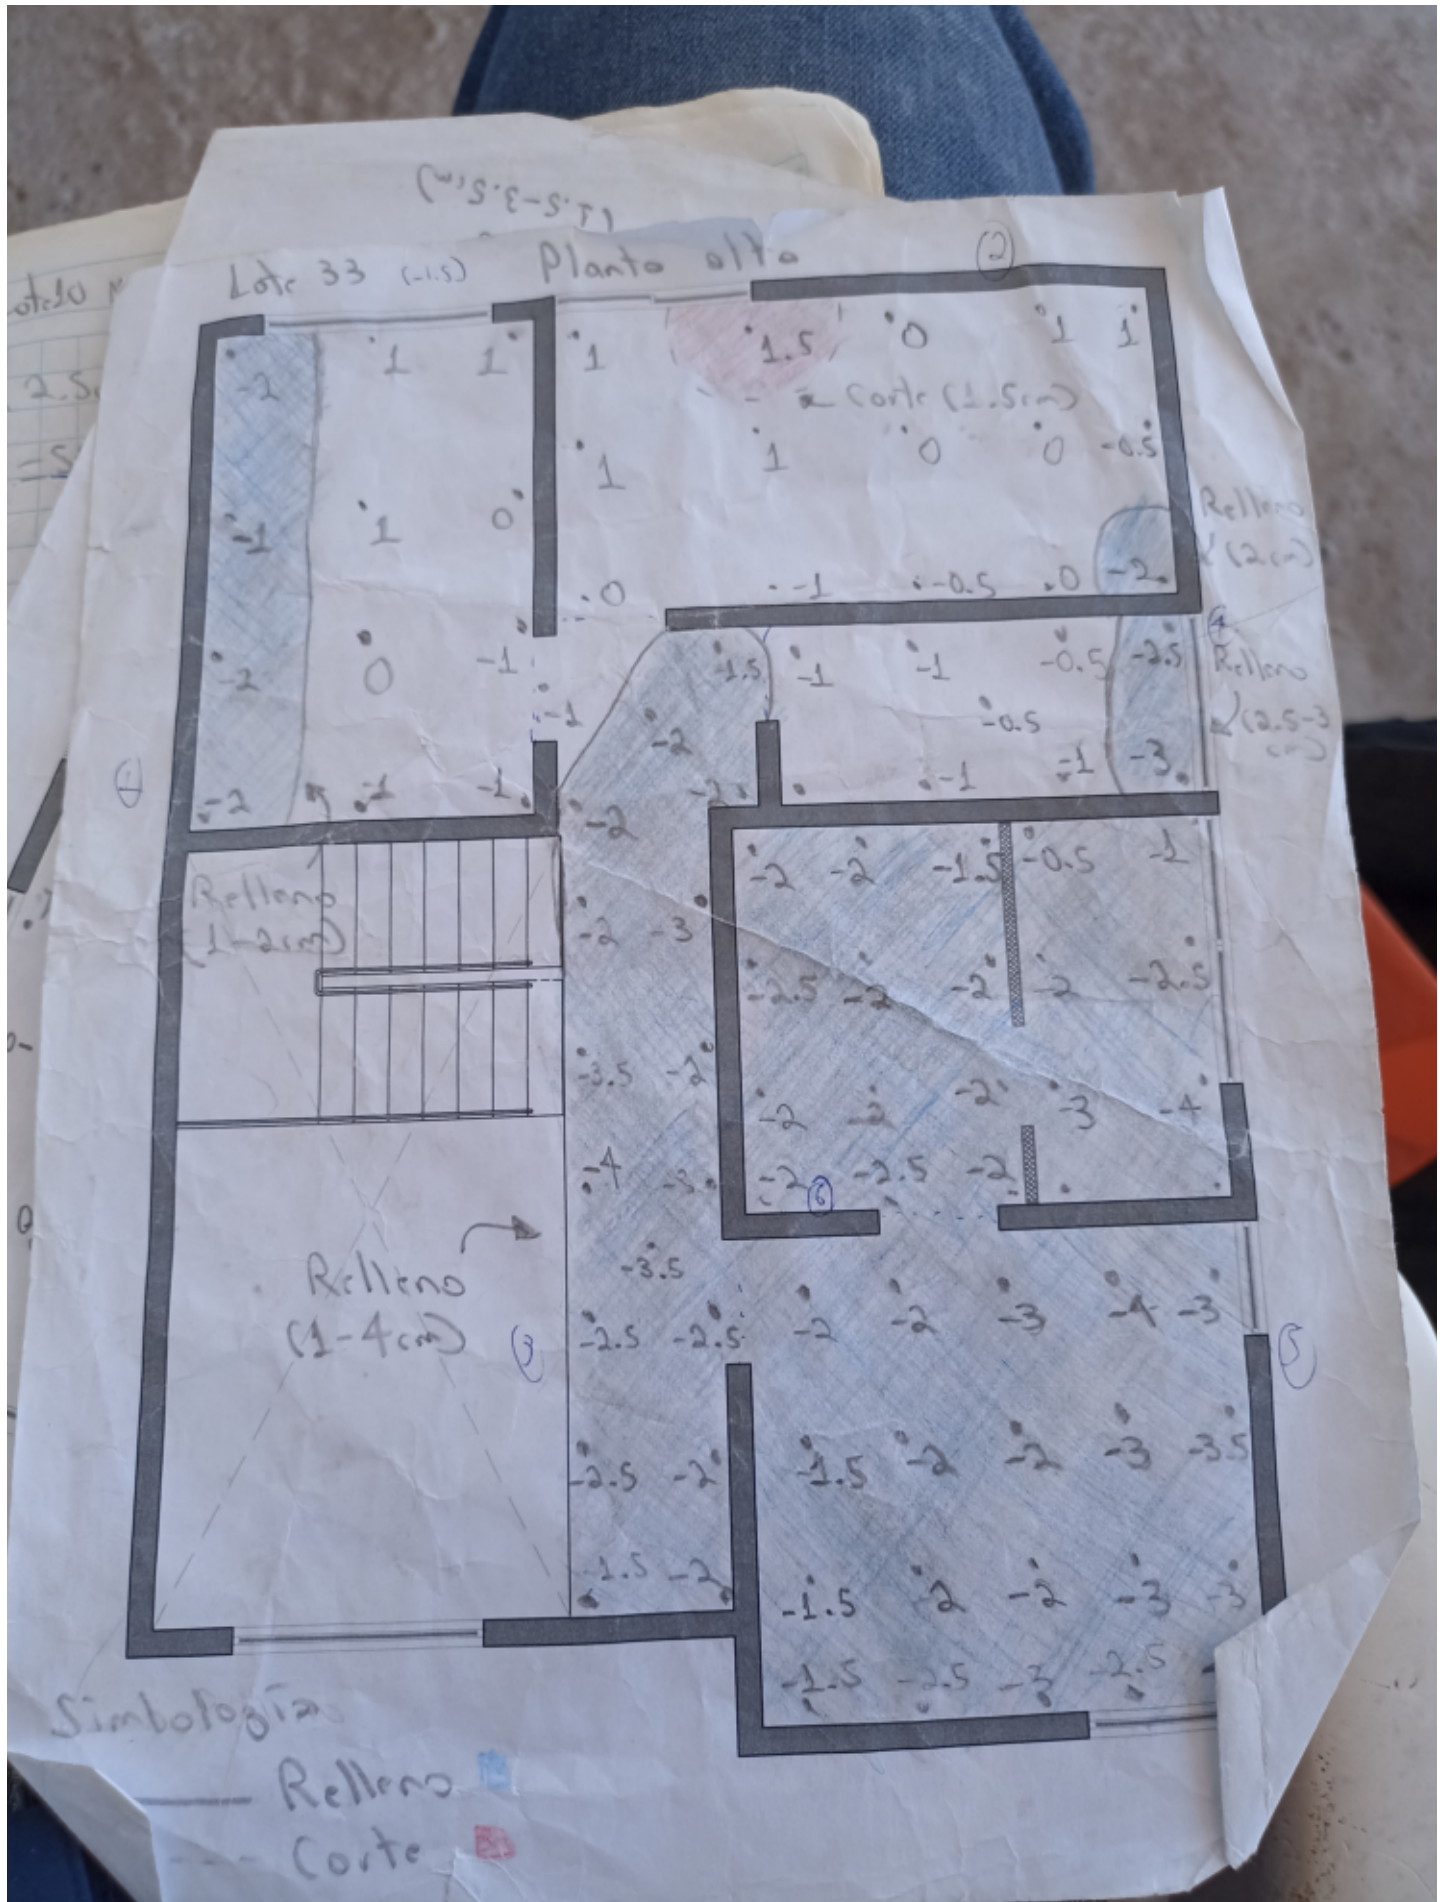


LOTE 9 · MZA 7 (MERLOT) — PLANTA BAJA

Hoja digitalizada · 74.86 m² · prom. 3.10 cm · mortero 2.56 m³ · hoja: V=2.56 m3




● Relleno (cota -) ● Corte (cota +) ● A nivel (0) ▨ Escalera (hueco)

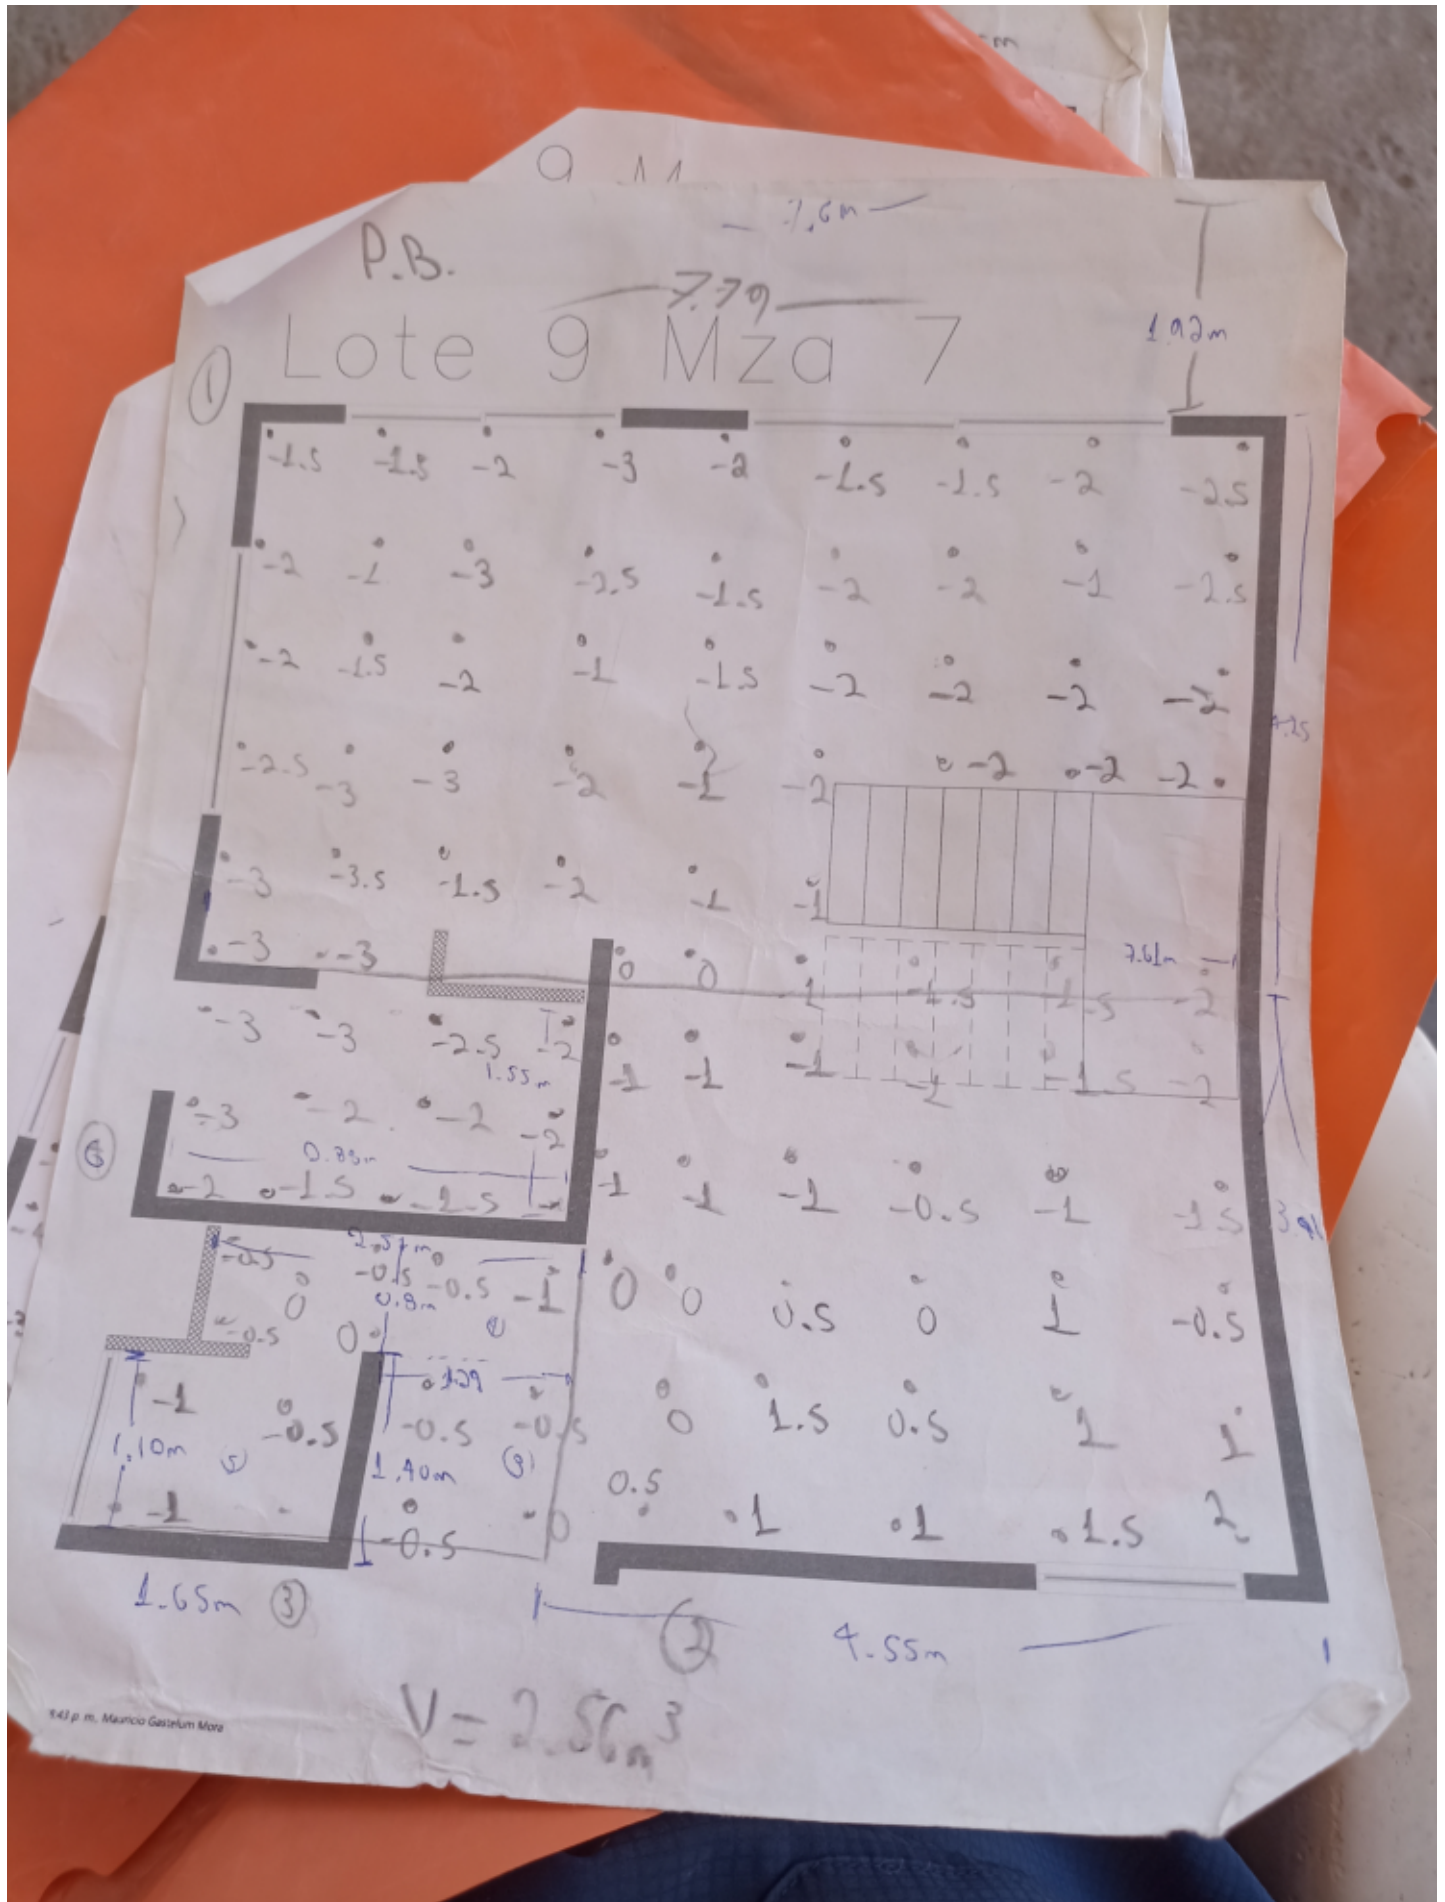

LOTE 9 · MZA 7 (MERLOT) — PLANTA ALTA

Hoja digitalizada · 58.25 m² · prom. 3.40 cm · mortero 1.93 m³ · hoja: V=1.93 m3

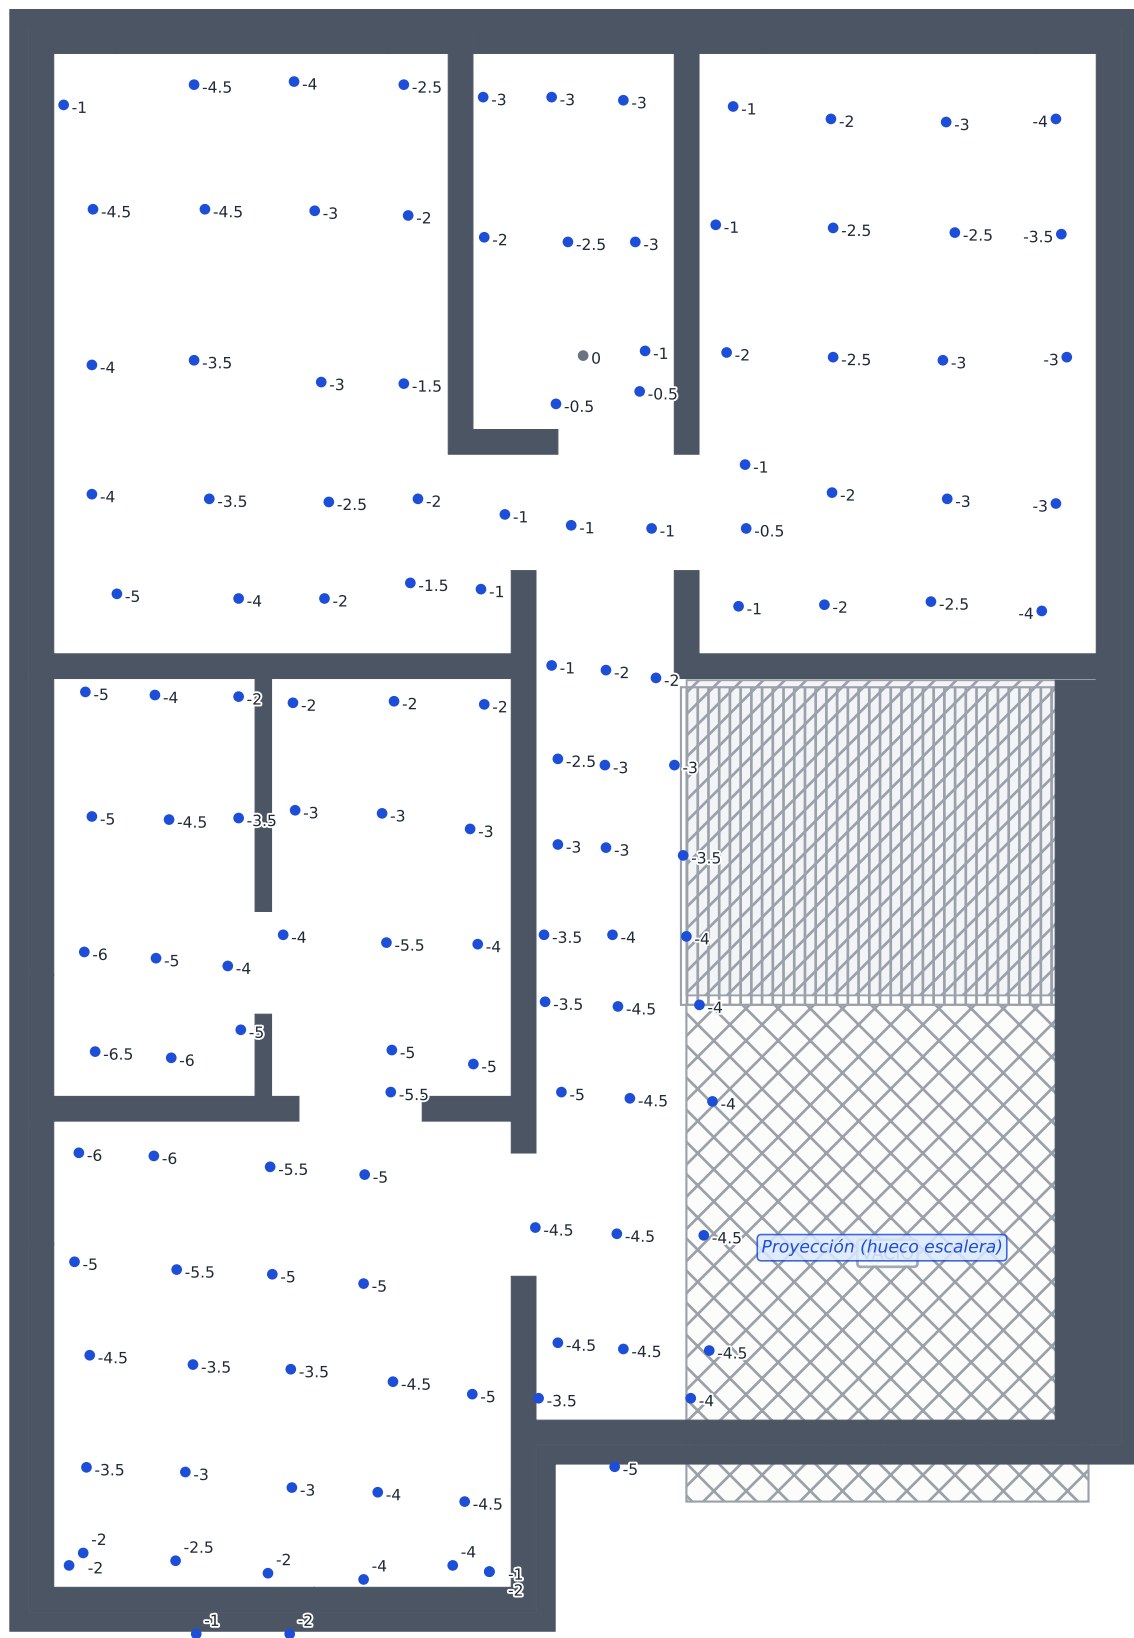


● Relleno (cota -) ● A nivel (0) ▨ Escalera (hueco) ▨ Vacío / sin losa




LOTE 10 · MZA 7 (MERLOT) — PLANTA BAJA

Hoja digitalizada · 74.86 m² · prom. 1.20 cm · mortero levantada, sin ejecutar · hoja: V=1.06 m3

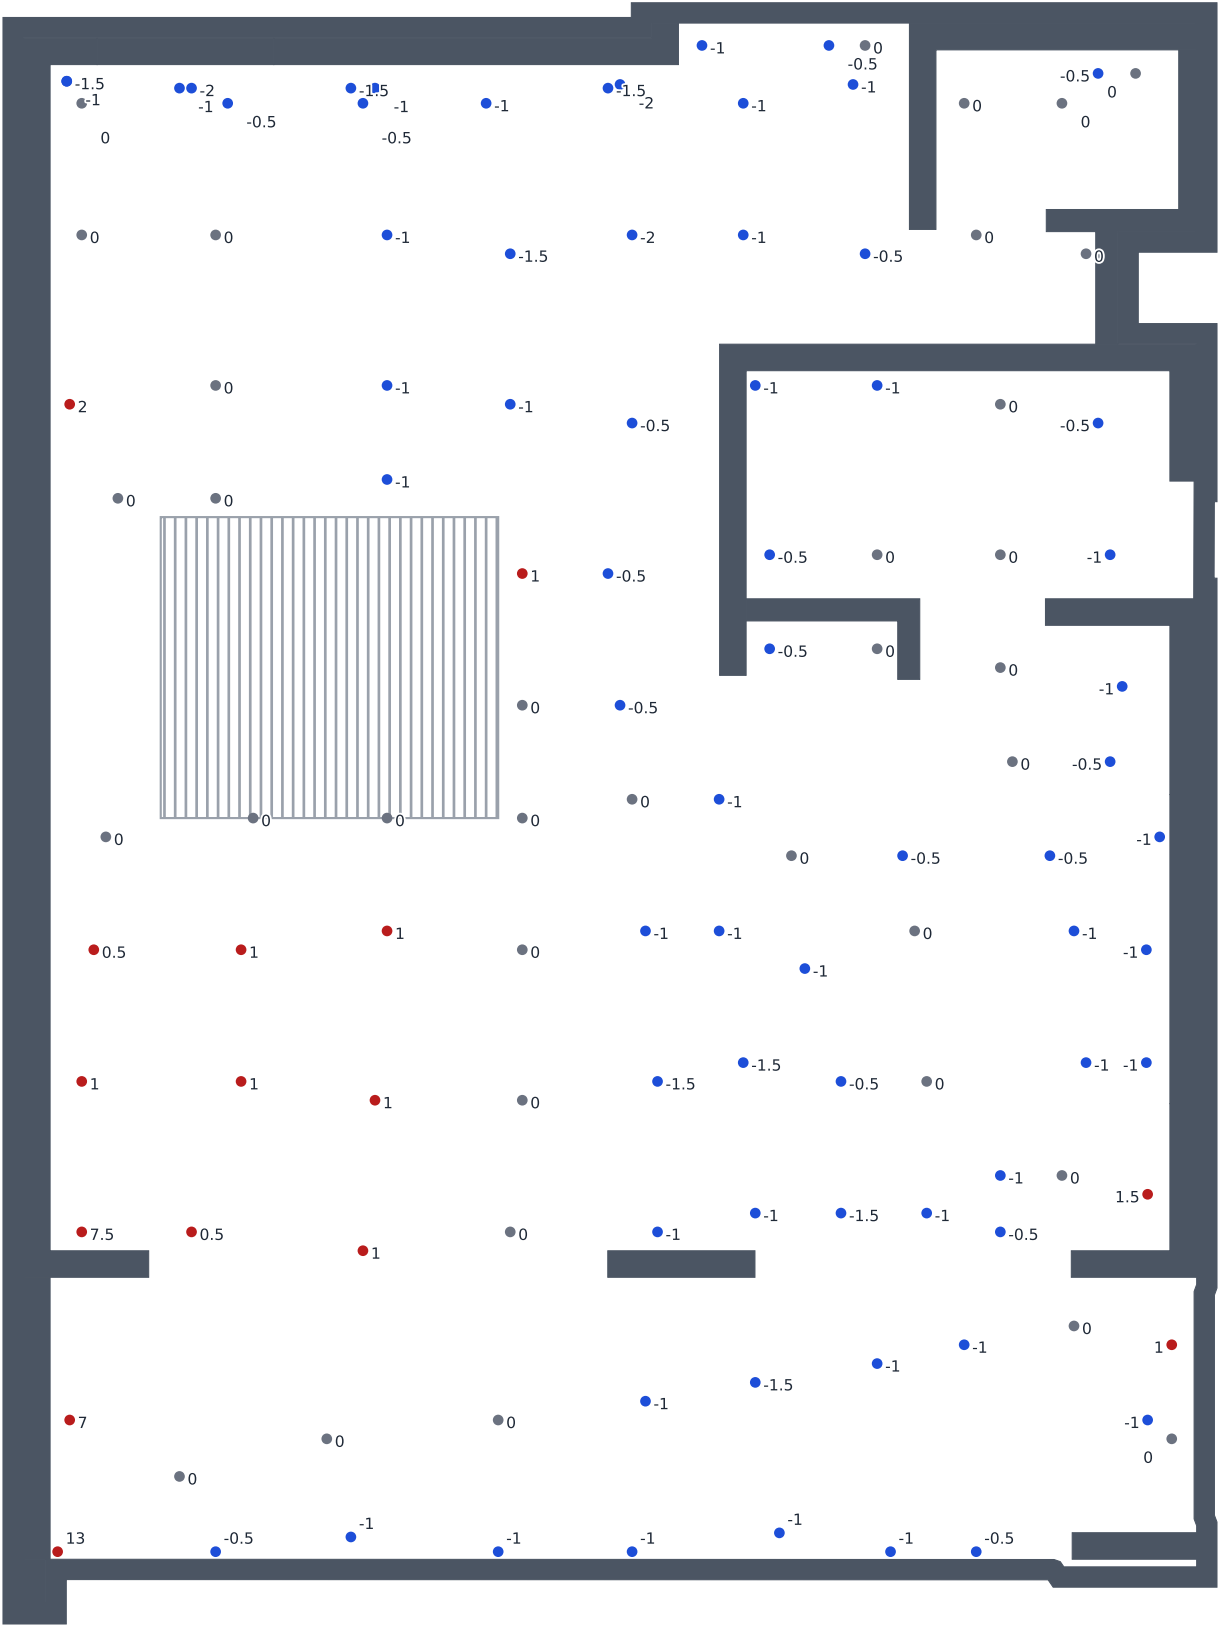


● Relleno (cota -) ● Corte (cota +) ● A nivel (0) ▨ Escalera (hueco)

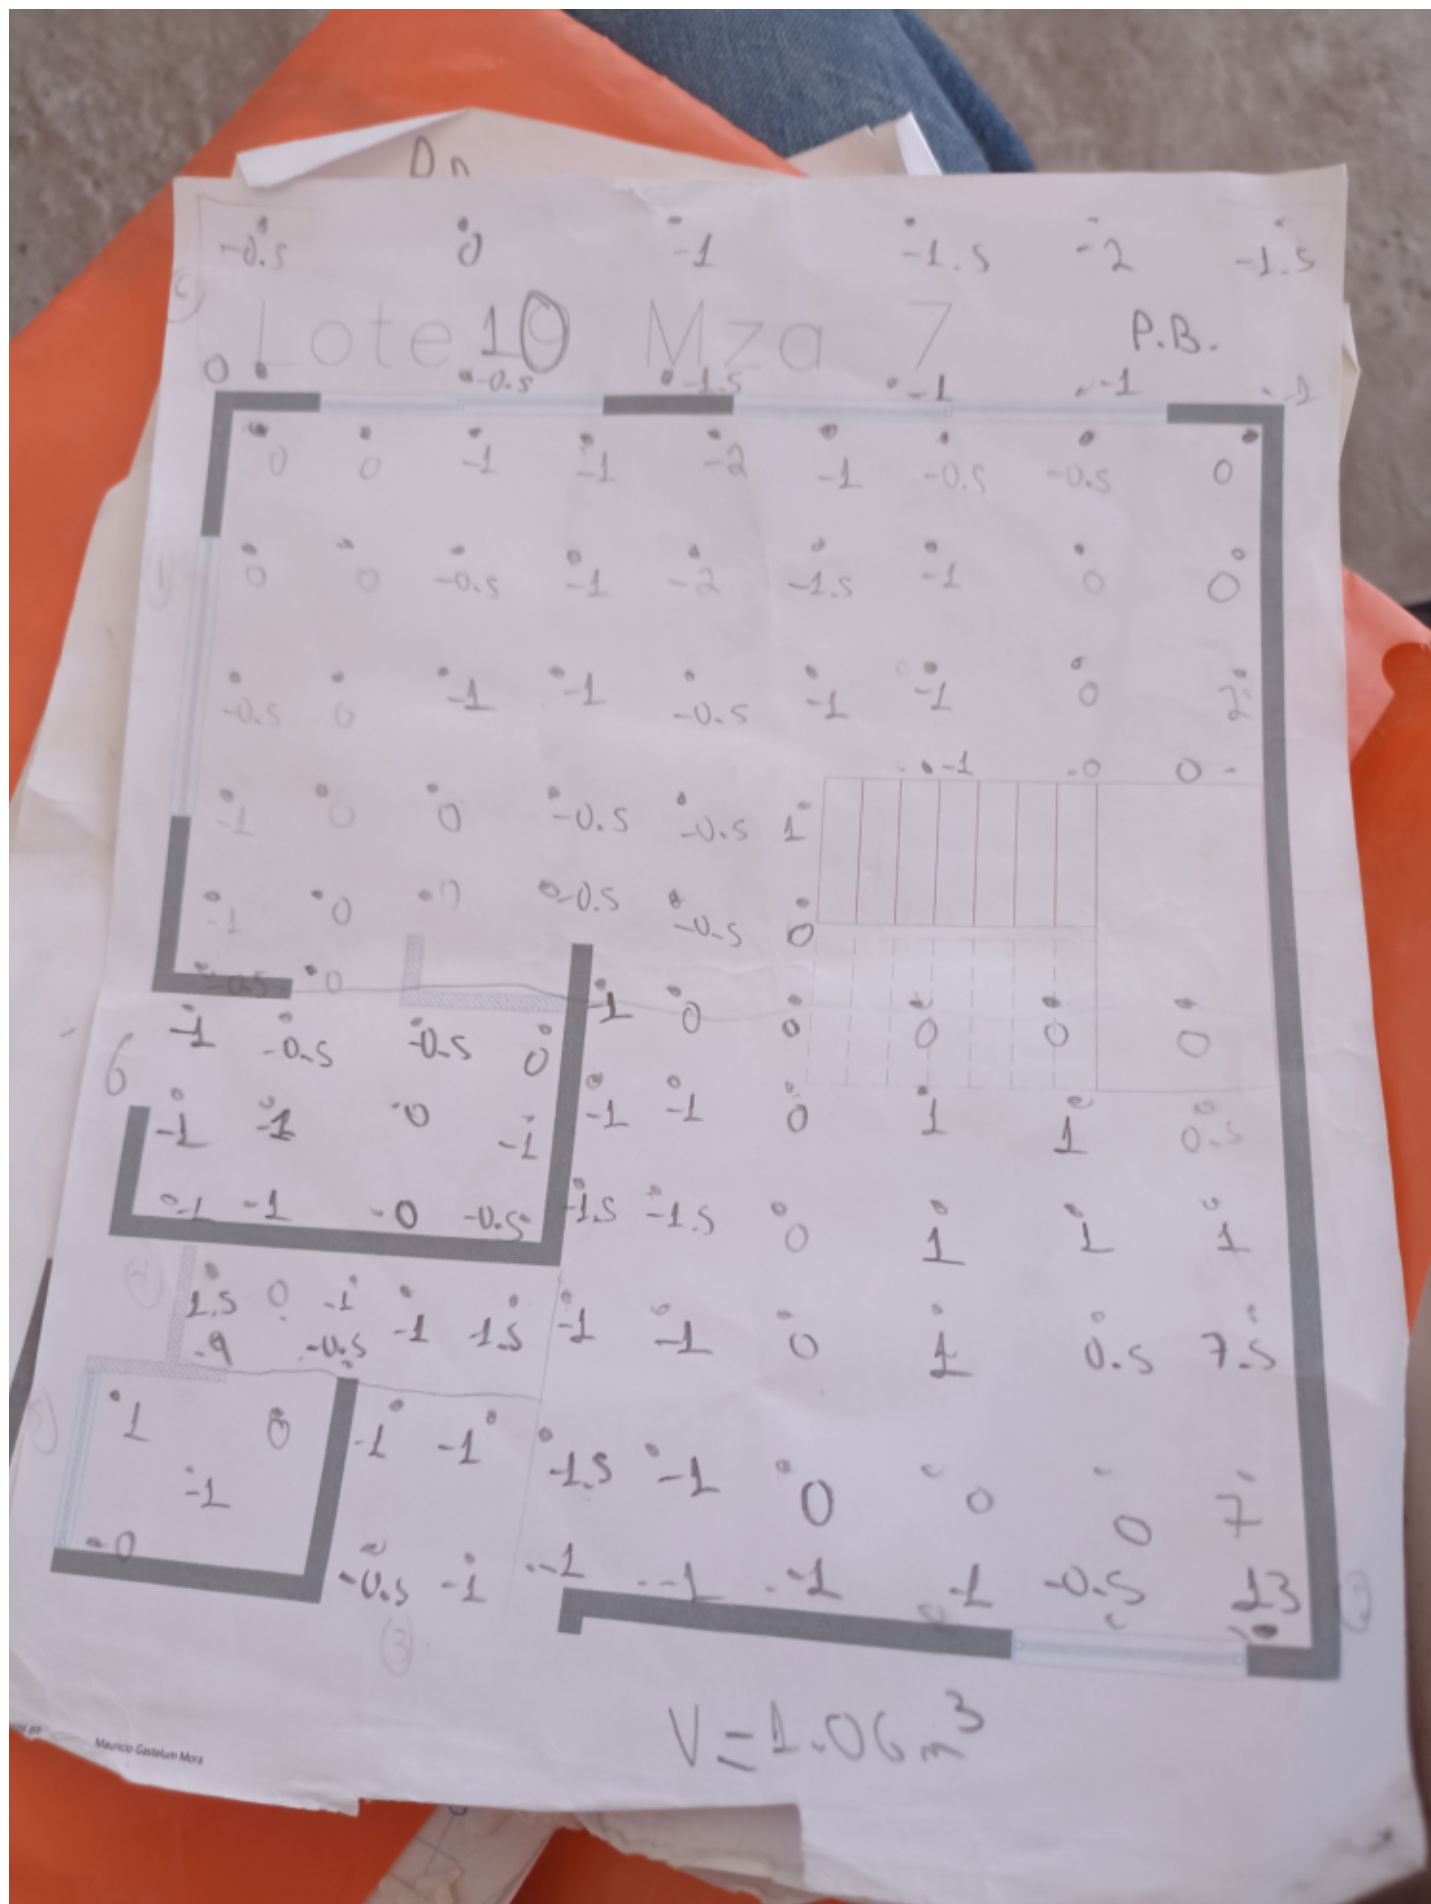


LOTE 10 · MZA 7 (MERLOT) — PLANTA ALTA

Hoja digitalizada · 58.25 m² · prom. 2.50 cm · mortero 1.50 m³ · hoja: V=1.46 m3

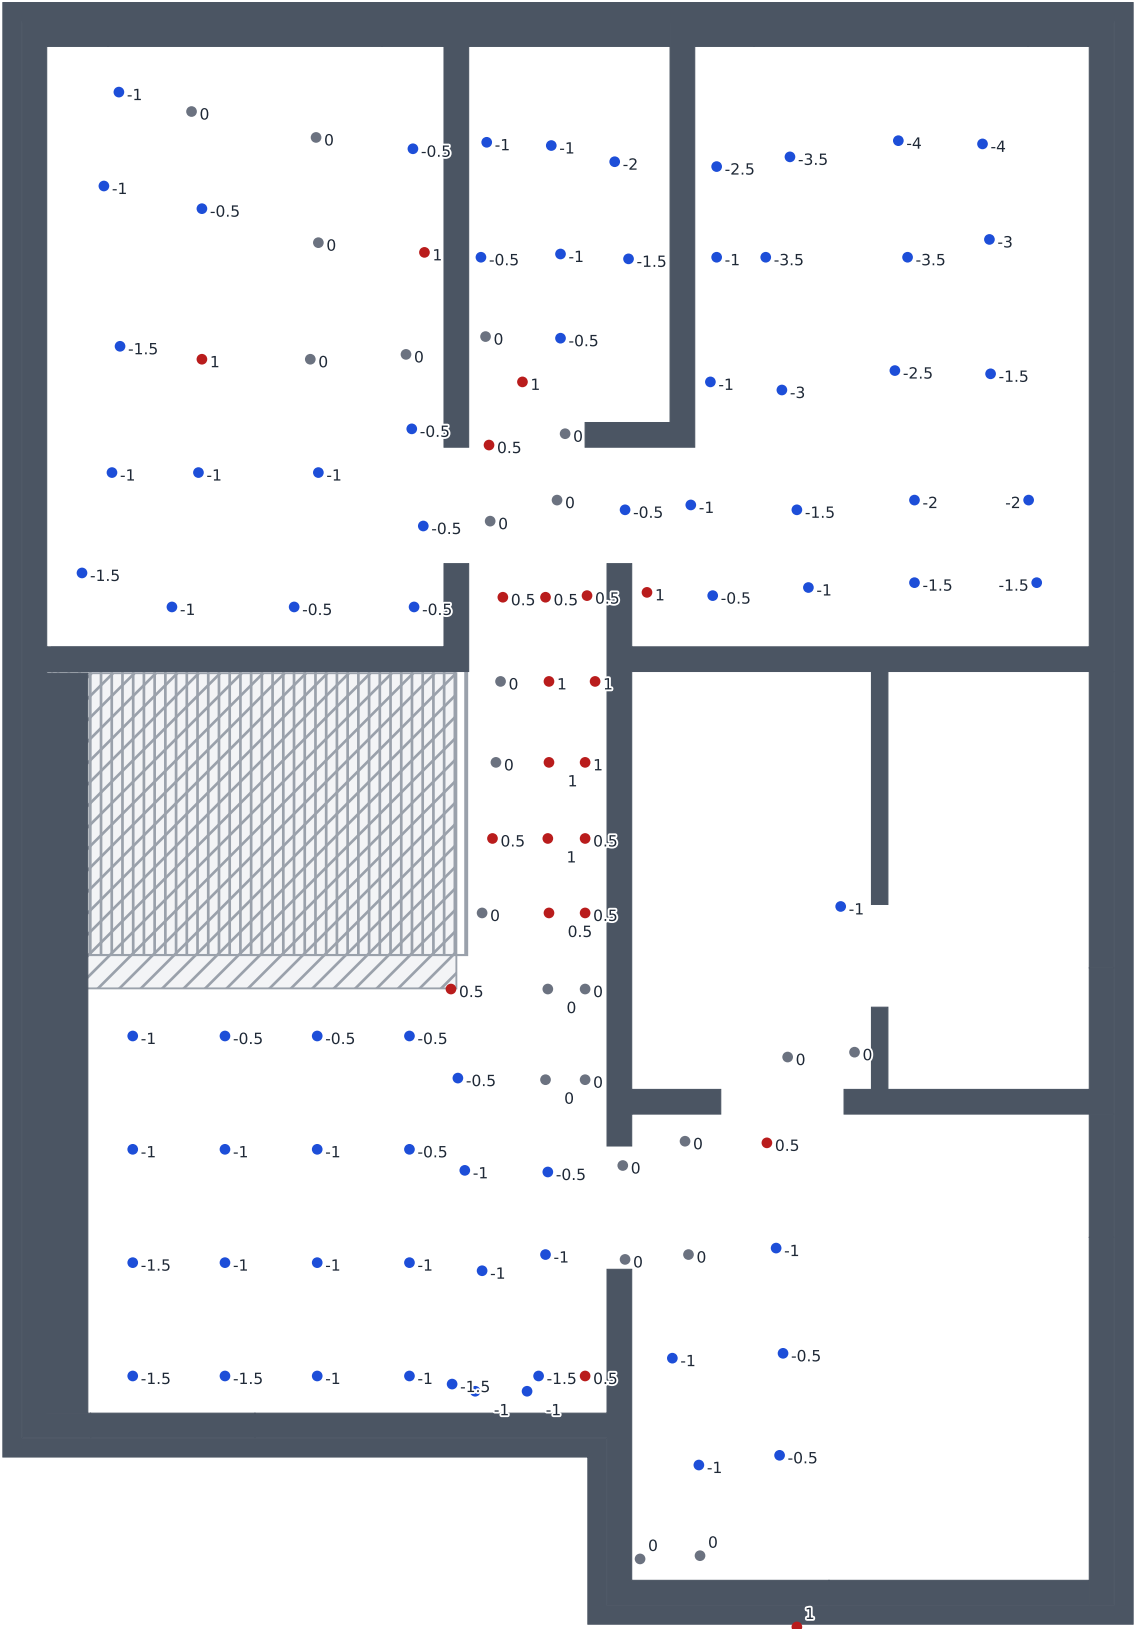


● Relleno (cota -) ● Corte (cota +) ● A nivel (0) ▨ Escalera (hueco)

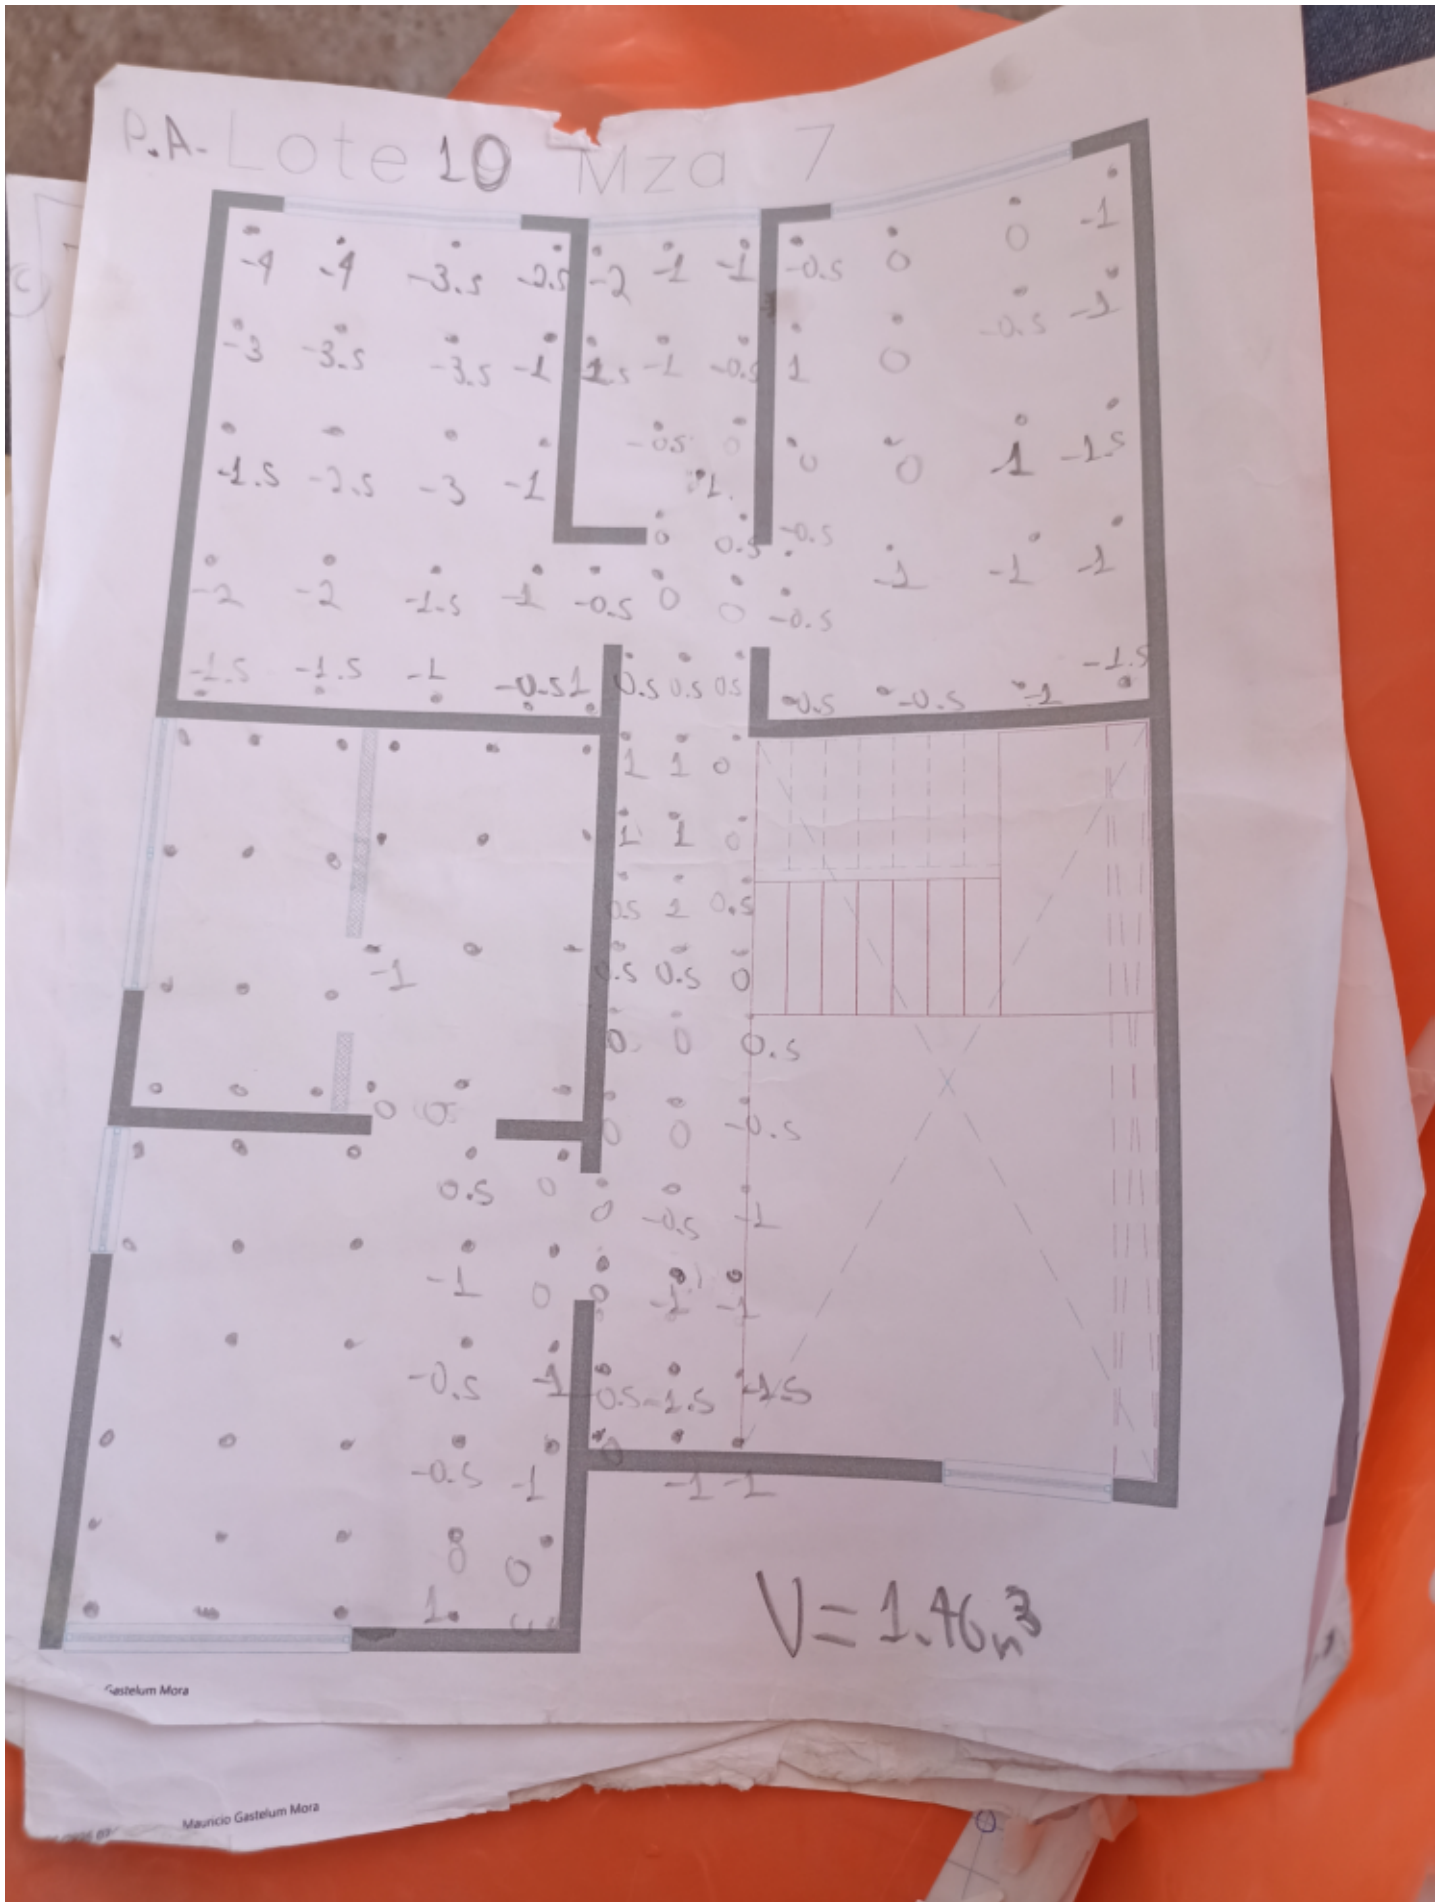


LOTE 19 · MZA 7 (CHARDONNAY) — PLANTA BAJA

Hoja digitalizada · 85.79 m² · prom. 1.71 cm · mortero 1.46 m³

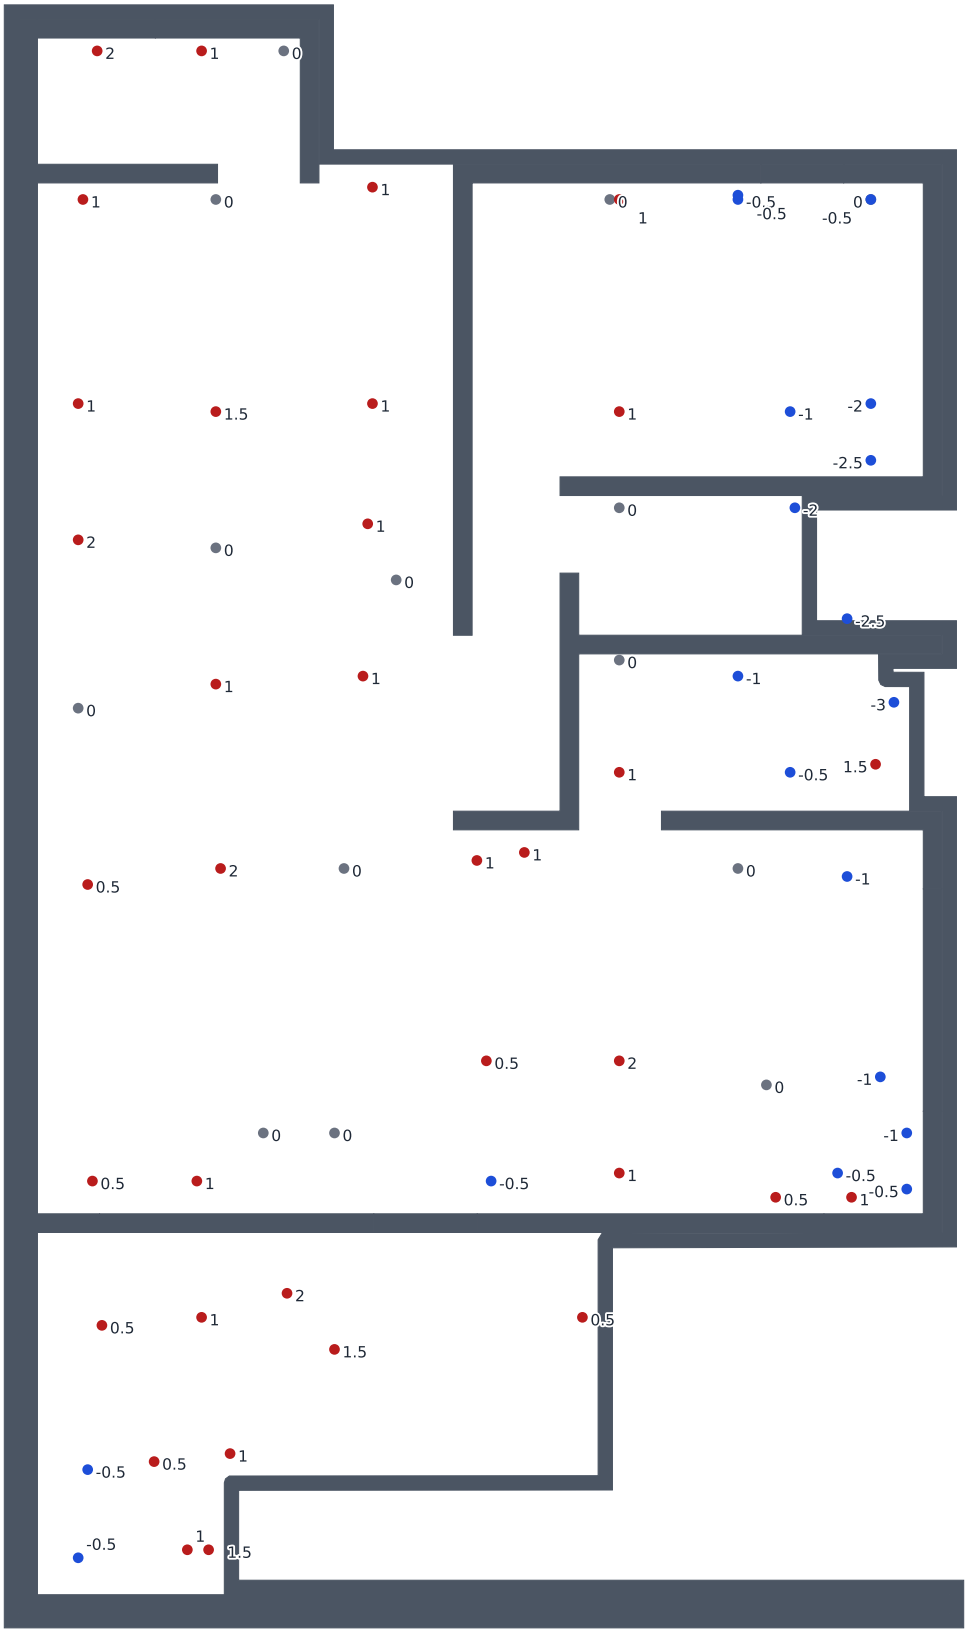

● Relleno (cota -) ● Corte (cota +) ● A nivel (0)

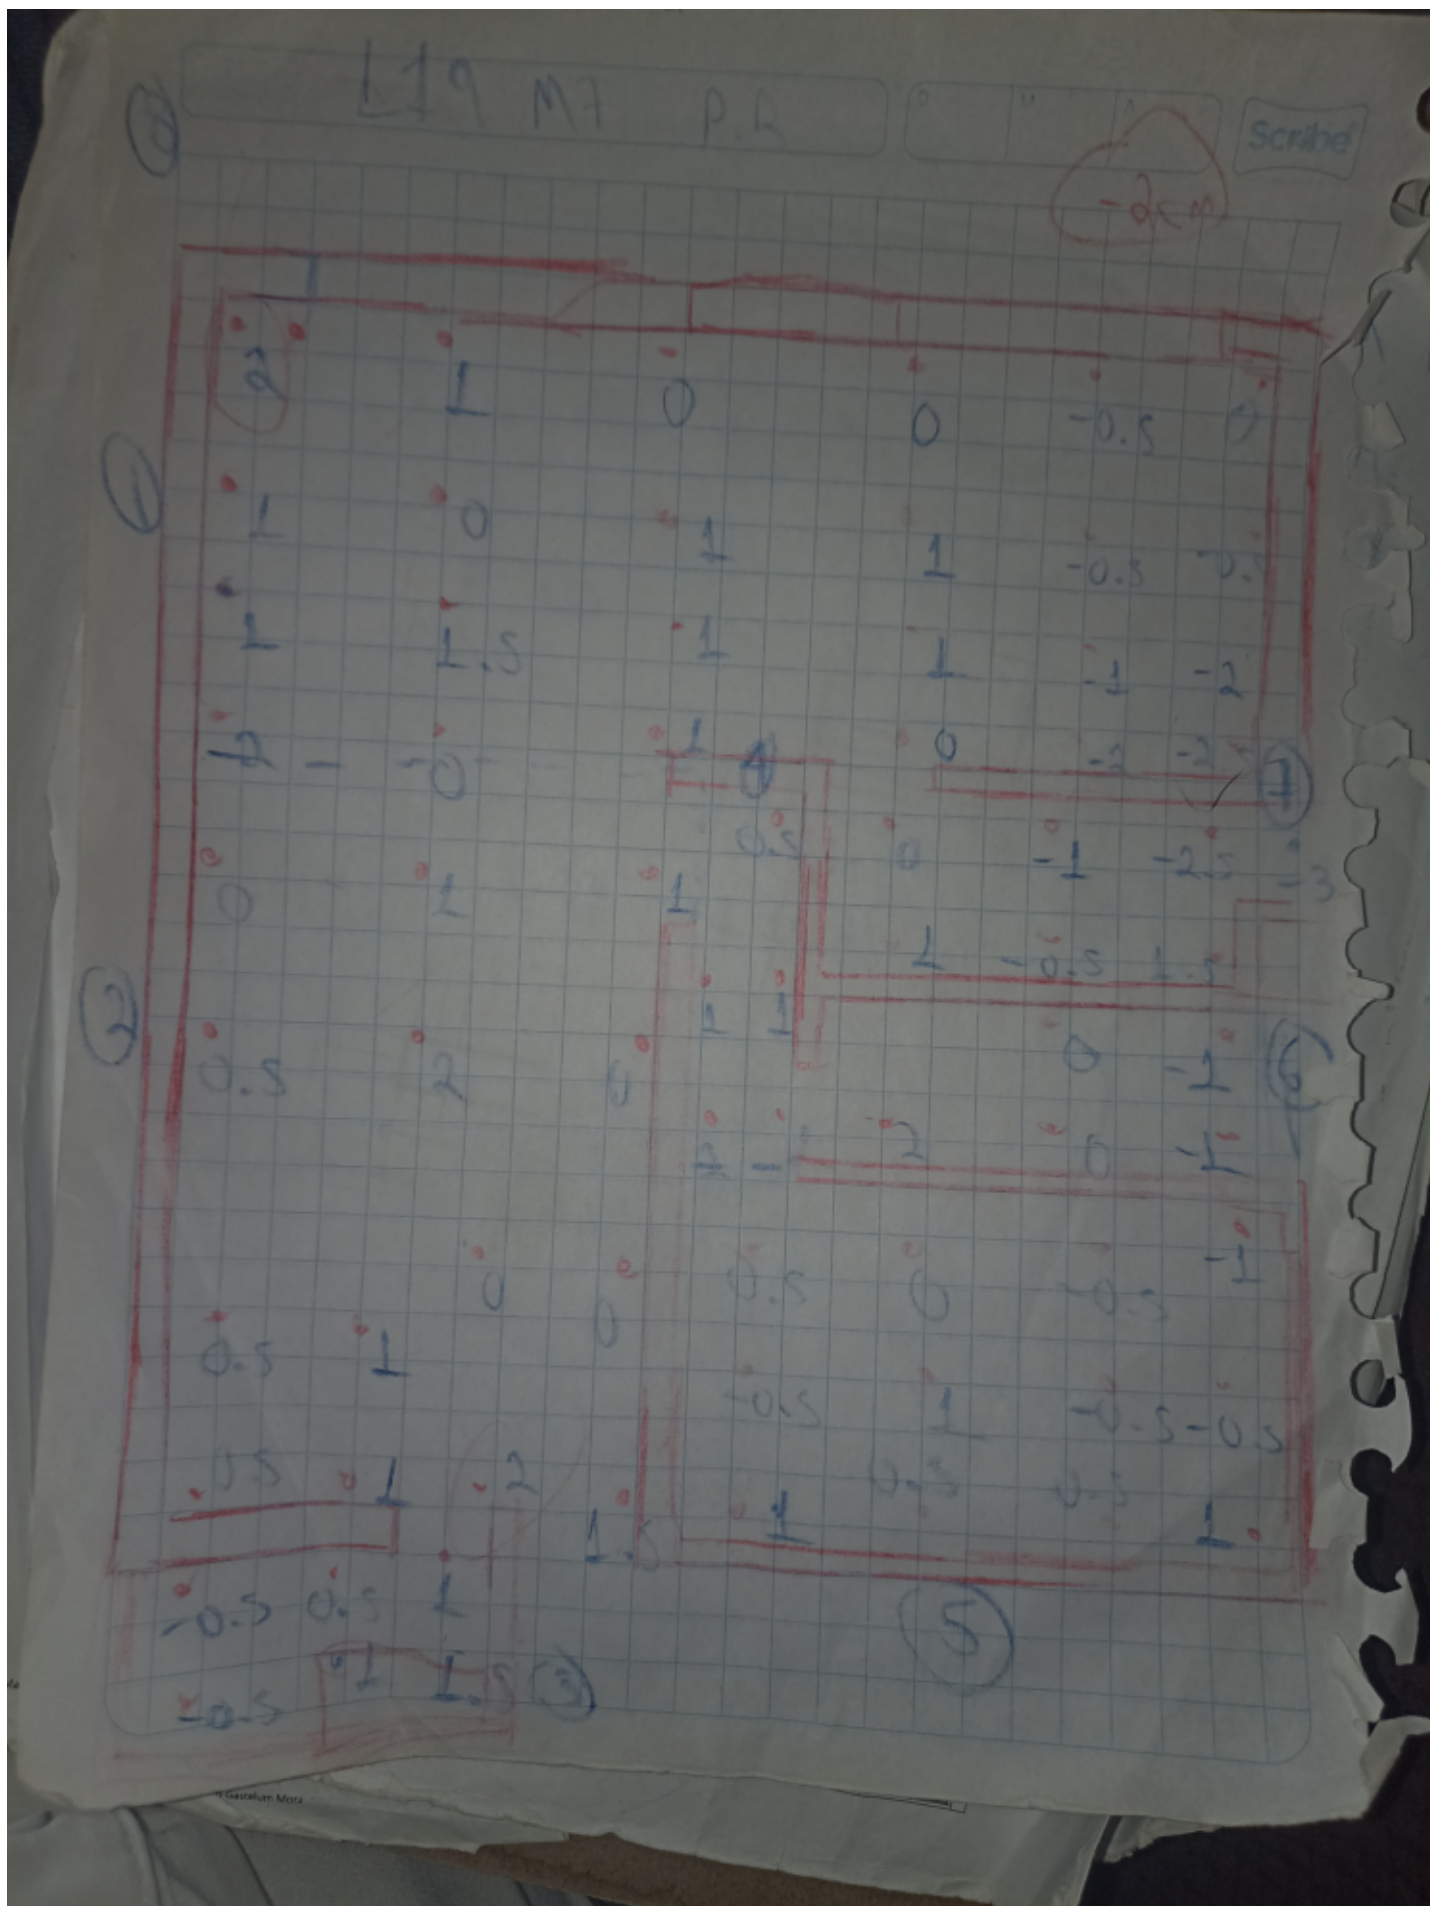

Hoja digitalizada · 59.86 m² · prom. 3.40 cm · mortero 1.50 m³




Hoja de campo original



Hoja digitalizada · 85.79 m² · prom. 1.45 cm · mortero 1.28 m³




● Relleno (cota -) ● Corte (cota +) ● A nivel (0) ▨ Escalera (hueco) ▩ Vacío / sin losa

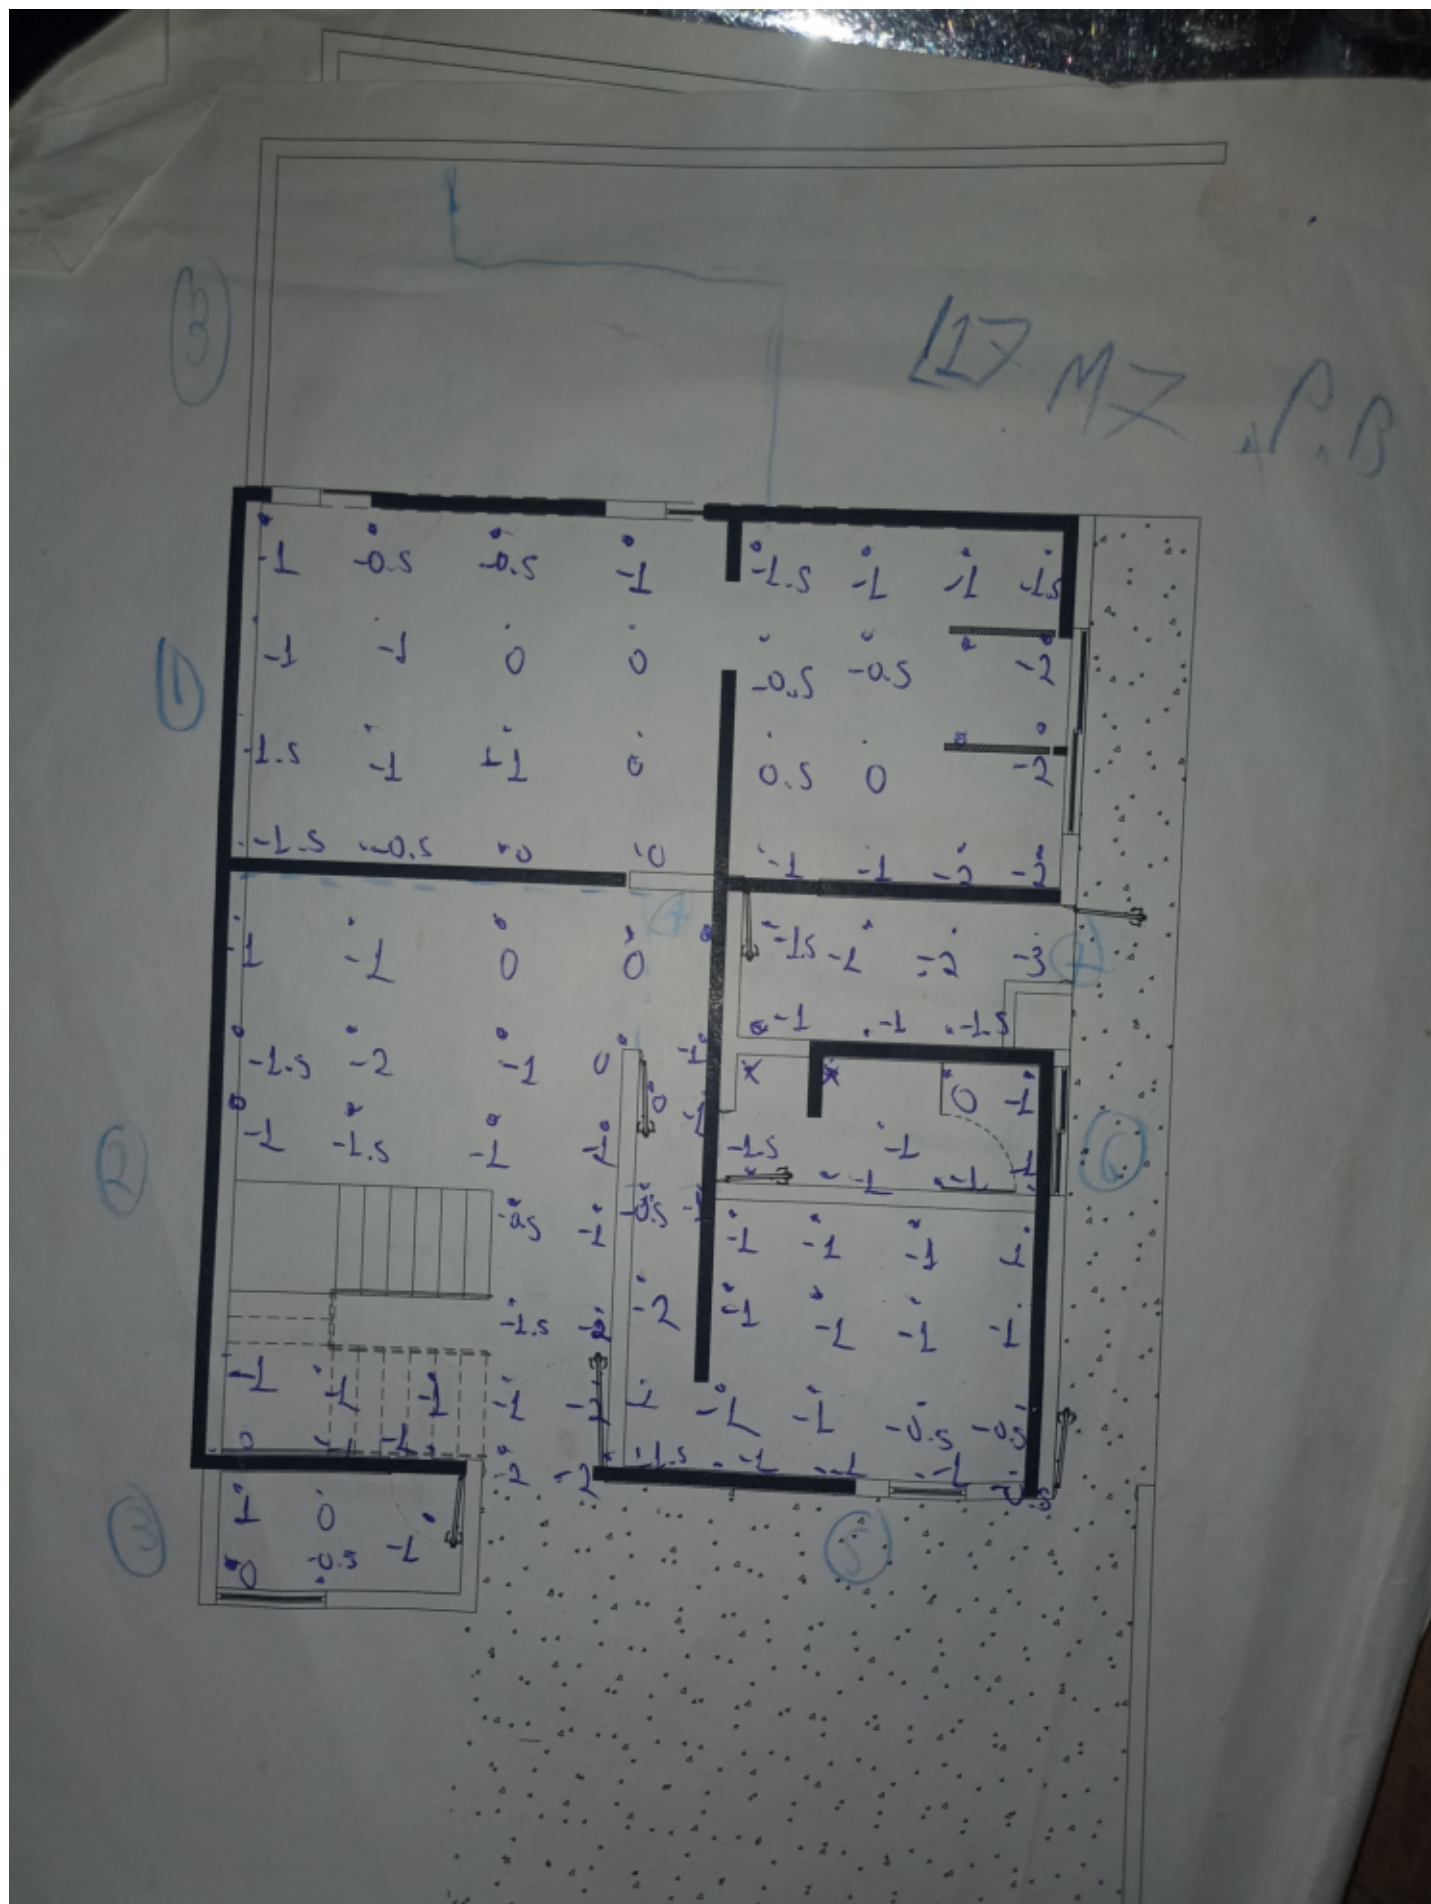

LOTE 17 · MZA 7 (CHARDONNAY) — PLANTA ALTA

Hoja digitalizada · 59.86 m² · prom. 2.24 cm · mortero 2.59 m³

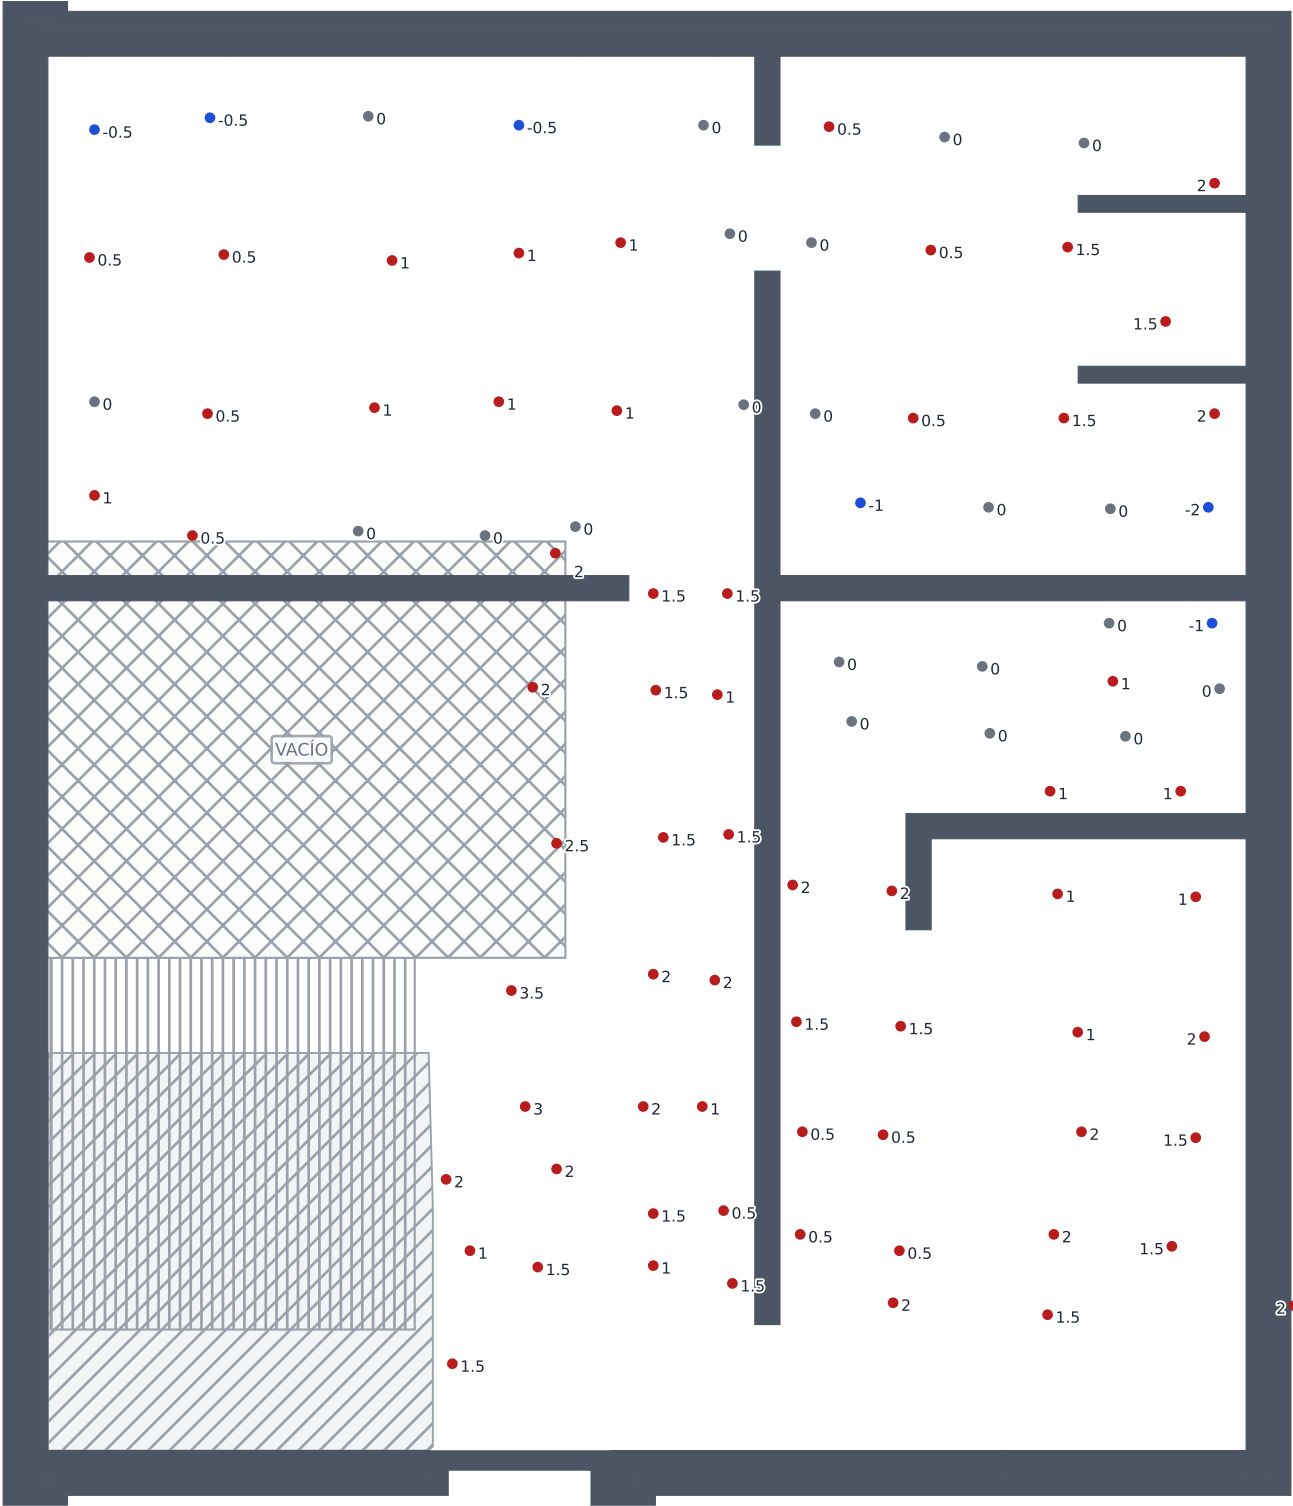

● Relleno (cota -) ● Corte (cota +) ● A nivel (0) ▨ Escalera (hueco) ▨ Vacío / sin losa

